640 ХҮҮХДИЙН СУРГУУЛИЙН НЭГ МАЯГИЙН БАРИЛГЫН ЗУРАГ ТӨСӨЛ

/ЗАГВАР ЗУРАГ/

ХЯНАСАН:

Үндсэн захиалагч:	Нэр	Гарын үсэг
Боловсролын яамны төрийн нарийн бичгийн дарга	Х.Батжаргал	
Захиалагч:		
Эдийн засаг, хөгжлийн яамны төрийн нарийн бичгийн дарга	И.Батхүү	
Барилгын хөгжлийн төв ТӨҮГ-ны зураг төслийн хяналтын хэлтсийн дарга	Г.Мөнхболд	
Зөвшөөрөлцсөн:		
ОБЕГ ГТТГ-н БЗХТасгийн дарга, Дэд хурандаа	Б.Мягмаржав	

МОНГОЛ УЛС
ОНЦГОЙ БАЙДЛЫН ЕРӨНХИЙ ГАЗАР
ХЯНАСАН
20 25 ОНЫ 12 САРЫН 29-НИЙ ӨДӨР
ГАРЫН ҮСЭГ:

БОЛОВСРУУЛСАН:

Албан тушаал	Нэр	Гарын үсэг
"Гипотенуз Дизайн" ХХК-ийн захирал	М.Энхтөр	

ГИПОТЕНУЗ ДИЗАЙН ХХК
9021050400 670147 СБТ14949
УЛААНБААТАР ХОТ

Улаанбаатар хот
2025 ОН

ЗУРАГ ТӨСӨЛ ЗОХИОГЧИЙН ТУСГАЙ ЗӨВШӨӨРЛИЙН ХУУЛБАР

0009304

БАРИЛГА, ХОТ БАЙГУУЛАЛТЫН ЯАМ

ТУСГАЙ ЗӨВШӨӨРӨЛ

_____ Дугаар... ЗТ12-896/21

"Аж ахуйн үйл ажиллагааны тусгай зөвшөөрлийн тухай" Монгол Улсын хуулийг үндэслэн ..... Улаанбаатар ..... аймаг/нийслэлийн ..... Баянзүрх ..... сум/дүүргийн ..... "Гипотенуз дизайн" ХХК ..... -д

9011827492 /улсын бүртгэлийн дугаар/ 6701477 /регистрийн дугаар/

ЗТ-2.1, ЗТ-6.2 заалтын дагуу

Нэмэлтээр ЗТ-6.1, ЗТ-6.3, ЗТ-6.4 ЗТ-8.1 заалтын дагуу

Нэмэлтээр ЗТ-3.1, ЗТ-10.2 заалтын дагуу

..... ажил, үйлчилгээ эрхлэх тусгай зөвшөөрлийг 2021 оны 11 -р сарын 15 -ны өдрөөс таван жилийн хугацаатай олгов.

Тусгай зөвшөөрөл нь хавсралт болон гэрээний хамт хүчинтэй.

БАРИЛГА, ХОТ БАЙГУУЛАЛТЫН САЙД **Б.МӨНХБААТАР**

2021 он 11 сар 15 өдөр

Улаанбаатар хот

Hypotenuse Design LLC Барилгын зураг төслийн "ГИПОТЕНУЗ ДИЗАЙН" ХХК УТАС : 88014798	640 ХҮҮХДИЙН СУРГУУЛИЙН БАРИЛГЫН НЭГ МАЯГИЙН ЗУРАГ ТӨСӨЛ	НЭР	ГАРЫН ҮСЭГ	ЗАГВАР ЗУРАГ
	Гүйцэтгэгч: "Гипотенуз Дизайн" ХХК-н захирал	М.Энхтөр		М1:200
	Гүйцэтгэгч: Архитектор	Б.Ариунзаяа		Хуудас-1
	Захиалагч: Боловсролын яамны ~~Сангүй~~ Хөрөнгө оруулалтын хэлтсийн дарга	Х.Тамираа		2025 он

ТӨЛӨВЛӨЛТИЙН САНАА

ЗАХИАЛАГЧИЙН ХҮСЭЛТ:

Барилгад байх анги танхим, өрөө тасалгаа,танхимуудыг "Ерөнхий боловсролын сургуулийн барилгын төлөвлөлт" БНбД 31-25-22 норм дүрмийн дагуу төлөвлөх,
хөгжлийн бэрхшээлтэй иргэдийн хэрэгцээ шаардлагад нийцүүлэх, үндсэн анги танхим зориулалтын өрөө тасалгааны байрлал, чиглэлийг нарны шууд тусгалын нормчлогдсон хугацаагаар хангах, хүүхэд чөлөөтэй сурч боловсрох нөхцөл бололцоог бүрэн хангасан байх, барилгын үндсэн хийц болон хашлага бүтээц, гадна дотор засалд хэрэглэх материал нь хүүхдийн эрүүл ахуйн шаардлага хангасан байх, барилгын төлөвлөлт гадна өнгө төрх хүүхдийн сонирхол татахуйц орчин үеийн шийдэлтэй байх зэрэг байна. Бусад холбогдох норм дүрэм стандартад нийцүүлэн төлөвлөх шаардлагатай.

АРХИТЕКТУРЫН ШИЙДЭЛ, СУДАЛГАА:

Төлөвлөж буй 640 хүүхдийн сургуулийн барилга нь 70.7м х 56м бүхий хэмжээтэй зоорийн давхартай, 3 давхар байна. Үндсэн 28 анги танхимтай, багш ажилчдын ажиллах орчин нөхцлийг хангах, сургуулийн үндсэн үйл ажиллагааг бүрэн хангахуйц байдлаар шийдэж сургуулийн норм дүрэм болон бусад шаардлагатай норм дүрэм стандартад нийцүүлэн төлөвлөсөн болно. Анги танхимд нарны гэрэл шууд тусахаар байрлуулсан да сургуулийн барилгад спортын зориулалт бүхий 2 заалтай мөн нэмэлтээр 2019 онд батлагдсан боловролын сургалтын хөтөлбөрийн дагуу зохион бүтээх өрөө болон бага боловсролын сургалтын хөтөлбөрийн дагуу спортын тусдаа заалтай төлөвлөсөн. урлаг үндсэн спорт заал номын сан зэрэг олноор цугларах хэсгийг 1 блок хэсэгт төлөвлөж анги танхимаас тусдаа байрлахаар төлөвлөсөн. Онцгой байдлын үед барилгаас гадагш чиглэсэн 9 гарц төлөвлөсөн бөгөөд үүний 3-н тусшай хэрэгцээт гарц бөгөөд 1-н техникийн зориулалт бүхий гарц 5-н ослын үеийн гарц байна.
Ялгаатай хэрэгцээтэй хүүхдүүдийг суралцах хөгжих үйлийг дэмжих ганцаарчилан хичээллэх анги мөн зорчих үйлийг хөнгөвчилсөн цахилгаан шат, ариун цэврийн хүүхдийн насны онцлогоор хүртээмжтэй байдлаар төлөвлөсөн.
Гадна спорт талбай болон тоглоомын талбайг БНбД 31-25-22 нормын дагуу насны онцлог бүрээр нь ялган талбай төлөвлөсөн.

Орчны судалгаа: 1 маяг

Хийцлэл: Төмөр бетон карказ бүхий хөнгөн блокон ханатай хөнгөн цагаан метал фасадтайгаар төлөвлөсөн.

Хэв маяг: Модерн

Онцлог уялдаа:

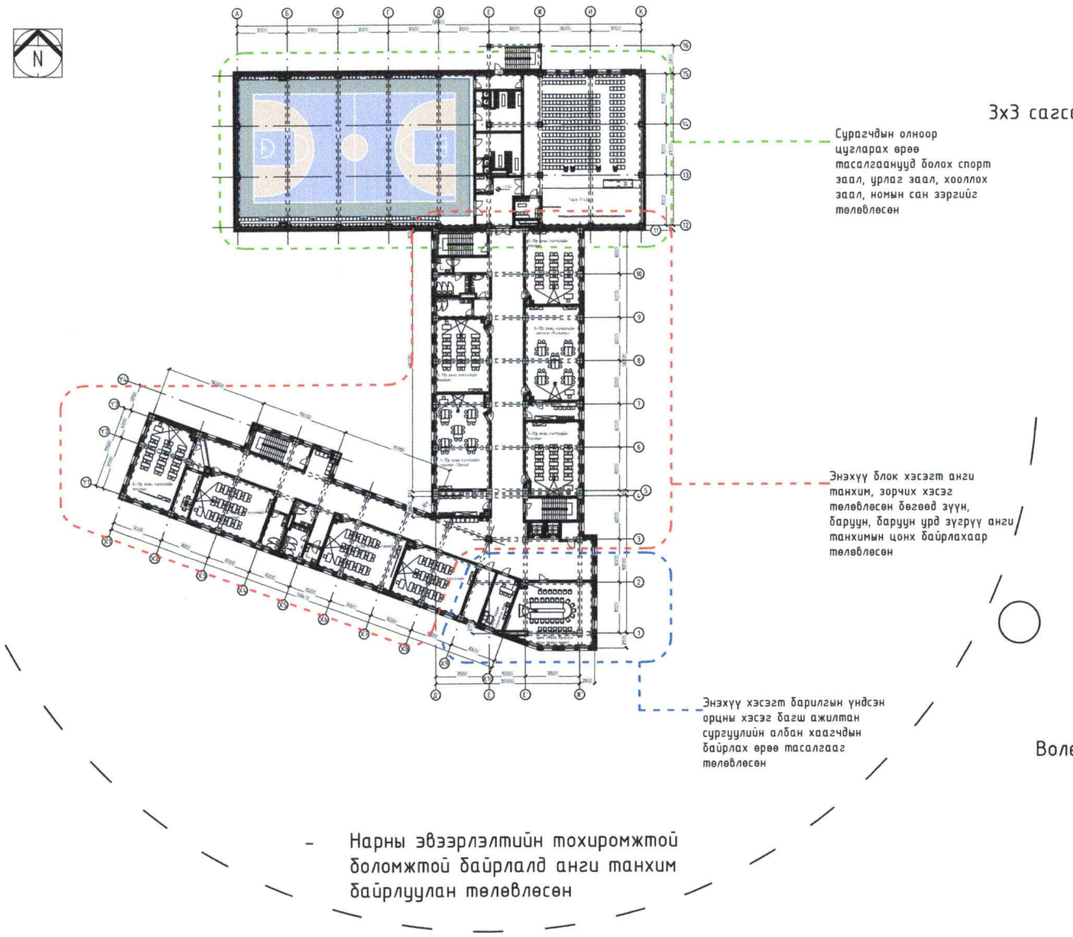

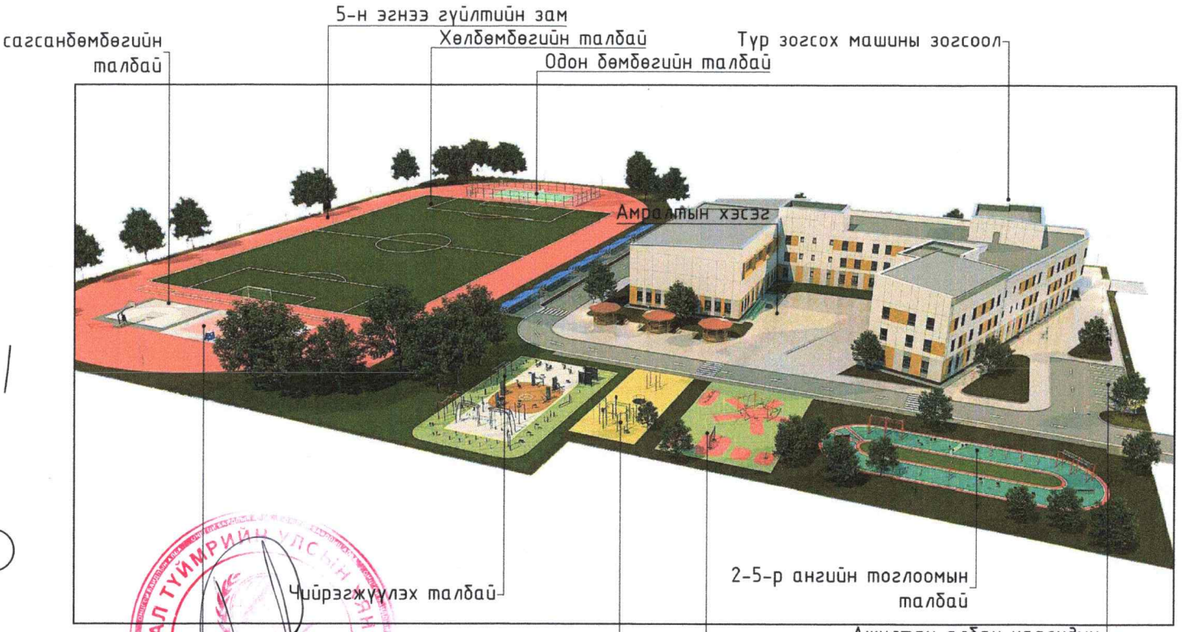

HYPOTENUSE DESIGN LLC Барилгын зураг төслийн "ГИПОТЕНУЗ ДИЗАЙН" ХХК УТАС : 88014798	640 ХҮҮХДИЙН СУРГУУЛИЙН БАРИЛГЫН НЭГ МАЯГИЙН ЗУРАГ ТӨСӨЛ	НЭР	ГАРЫН ҮСЭГ	ЗАГВАР ЗУРАГ
	Гүйцэтгэгч: "Гипотенуз Дизайн" ХХК-н захирал	М.Энхтөр		М1:200
	Гүйцэтгэгч: Архитектор	Б.Арцунзаяа		Хуудас- 2
	Захиалагч: Боловсролын яамны Санхүү, хөрөнгө оруулалтын хэлтсийн дарга	Х.Тамираа		2025 он

НАРНЫ ЭЭВЭРЛЭЛТ

3 ДУГААР САРЫН 22-НД

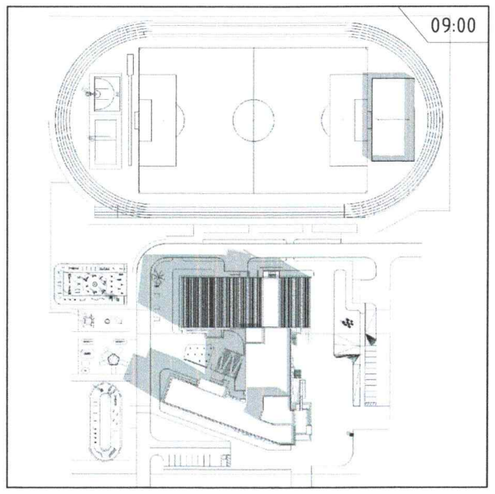

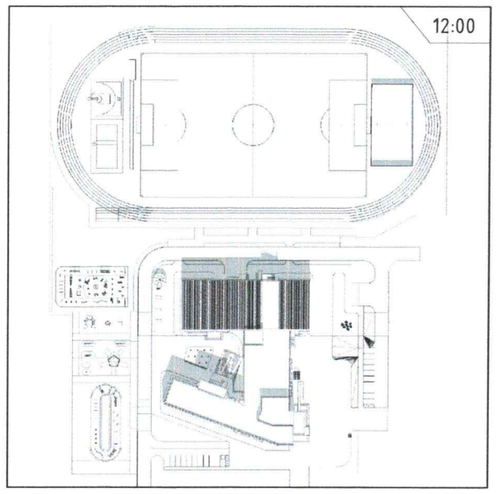

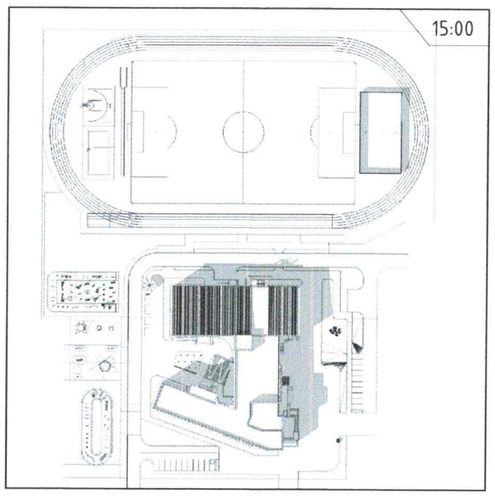

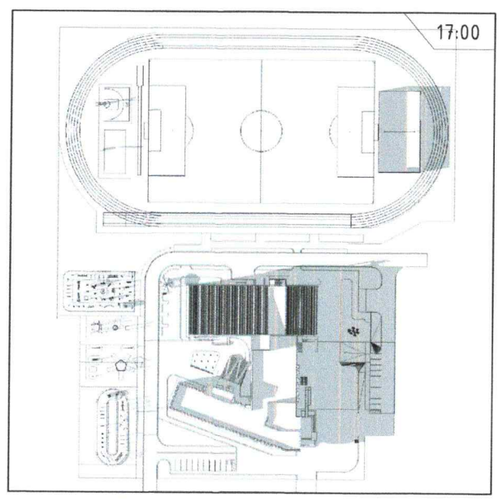

9 ДУГААР САРЫН 22-НД

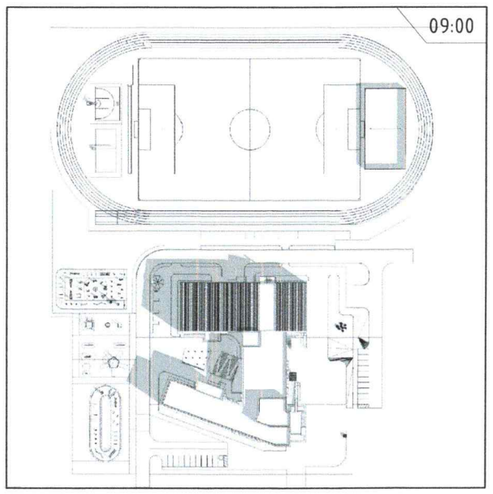

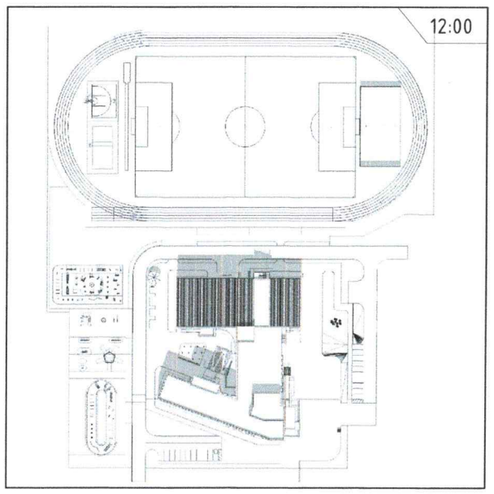

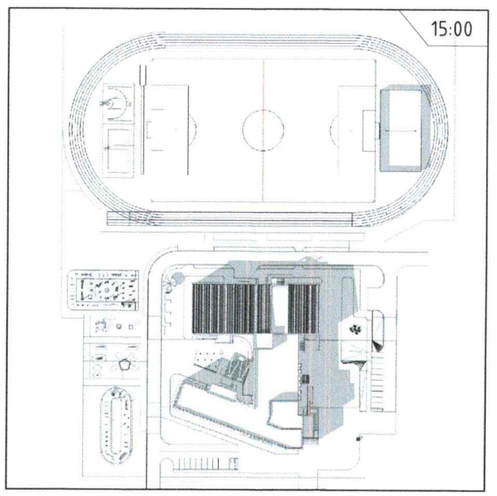

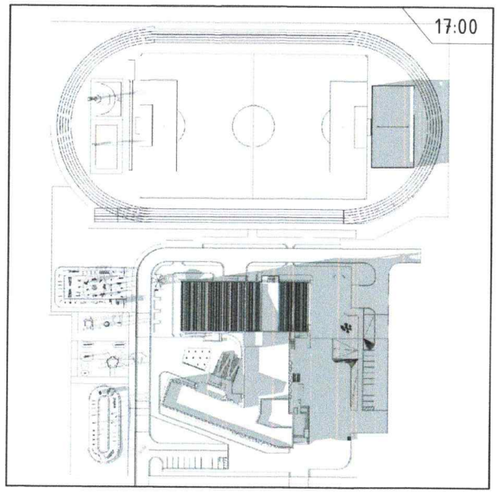

САЛХИНЫ ЗОНХИЛОХ ЧИГЛЭЛ /УЛААНБААТАР ХОТ/

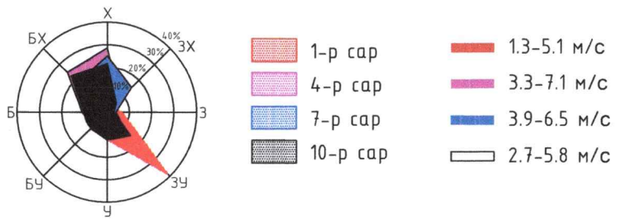

ӨГӨГДӨЛ:

Цаг уурын бүсчлэл: Цаг уурын IIа бүсэд хамрагдана.
Салхины зонхилох чиглэл: Баруун хойд, Хойд, Зүүн өмнөд зүгээс зонхилно.
Хур тунадас: Дулааны үе (IV-X сар) 236.5мм Хүйтний үе (XI-III сар) 12.3 мм
Газар хөдлөлтийн бүс: 8 балл
Дүгнэлт: 3 сарын 22, 9 сарын 22-ны өдрийн нарны ээвэрлэлтийн зураглалаар төлөвлөж буй буй барилгажилт дээр тусах ээвэрлэлт 4-с дээш цаг байгаа нь норм хангаж байна.

HYPOTENUSE DESIGN LLC Барилгын зураг төслийн "ГИПОТЕНУЗ ДИЗАЙН" ХХК УТАС : 88014798	640 ХҮҮХДИЙН СУРГУУЛИЙН БАРИЛГЫН НЭГ МАЯГИЙН ЗУРАГ ТӨСӨЛ	НЭР	ГАРЫН ҮСЭГ	ЗАГВАР ЗУРАГ
	Гүйцэтгэгч: "Гипотенуз Дизайн" ХХК-н захирал	М.Энхтөр		М1:200
	Гүйцэтгэгч: Архитектор	Б.Ариунзаяа		Хуудас- 3
	Захиалагч: Боловсролын яамны Санхүү, хөрөнгө оруулалтын хэлтсийн дарга	Х.Тамираа		2025 он

№	ТОДОРХОЙЛОЛТ	ТАЙЛБАР
1	Төлөвлөж сургуулийн барилга	Төлөвлөж буй
2	Төлөвлөж буй явган зам талбай	Төлөвлөж буй
3	Төлөвлөж буй авто зам, зогсоол	Төлөвлөж буй
4	Төлөвлөж буй тоглоомын талбай 2-5-р анги	Төлөвлөж буй
5	Төлөвлөж буй тоглоомын талбай 1-р анги	Төлөвлөж буй
6	Төлөвлөж буй тоглоомын талбай 6-9-р анги	Төлөвлөж буй
7	Төлөвлөж буй чийрэгжүүлэх талбай	Төлөвлөж буй
8	Төлөвлөж буй спортын талбай	Төлөвлөж буй

N ЕРӨНХИЙ ТӨЛӨВЛӨГӨӨ М 1:750

ТАНИХ ТЭМДЭГЛЭГЭЭ

- Төлөвлөж буй барилга, байгууламж
- Төлөвлөж буй авто зам (2315м2)
- Төлөвлөж буй явган хүний зам (4344м2)
- Төлөвлөж буй дугуйн зам
- Төлөвлөж буй авто зогсоол (17 ширхэг)
- Төлөвлөж буй зүлэгжүүлсэн талбай (3810м2)
- Архитектур төлөвлөлтийн даалгаврын схемийн хил хязгаар
- Эзэмшил газрын хил хязгаар
- Одоо байгаа барилга
- Одоо байгаа нураах барилга байгууламж
- Одоо байгаа явган хүний зам
- Одоо байгаа орон нутгийн чанартай авто зам
- Б — Бохир усны шугам
- Д — Дулааны шугам
- Ц — Цэвэр усны шугам
- Ц — Цахилгааны шугам

Барилгын зураг төслийн "ГИПОТЕНУЗ ДИЗАЙН" ХХК	640 ХҮҮХДИЙН СУРГУУЛИЙН БАРИЛГЫН НЭГ МАЯГИЙН ЗУРАГ ТӨСӨЛ	НЭР	ГАРЫН ҮСЭГ	ЗАГВАР ЗУРАГ
УТАС : 88014798	Гүйцэтгэгч: "Гипотенуз Дизайн" ХХК-н захирал	М.Энхтөр		М1:750
	Гүйцэтгэгч: Архитектор	Б.Арцүнзаяа		Хуудас-4
	Захиалагч: Боловсролын яамны Санхүү, хөрөнгө оруулалтын хэлтсийн дарга	Х.Тамираа		2025 он

ЗӨВШӨӨРӨЛЦСӨН:

Боловсролын яамны төрийн нарийн бичгийн дарга ..... / Х.Батжаргал /

Эдийн засаг, хөгжлийн яамны төрийн нарийн бичгийн дарга ..... / И.Батхүү /

ҮНДЭСЛЭЛ.
- Монгол Улсын 2024 оны төсвийн тухай хуулийн 2 дугаар хавсралт
- Шадар сайд бөгөөд Эдийн засаг, хөгжлийн сайдын 2024 оны 03 дугаар сарын 29-ний өдрийн А/12 дугаар тушаал.
- Хот тосгоны төлөвлөлт, барилгажилтын норм да дүрэм БНбД 30.01.04-ийн 1, 2, 4, 5 дугаар зүйлүүдийг үндэслэн ерөнхий төлөвлөгөөний зургийг гүйцэтгэв.

№	ТОДОРХОЙЛОЛТ	ТАЙЛБАР
1	Төлөвлөж сургуулийн барилга	Төлөвлөж буй
2	Төлөвлөж буй явган зам талбай	Төлөвлөж буй
3	Төлөвлөж буй авто зам, зогсоол	Төлөвлөж буй
4	Төлөвлөж буй тоглоомын талбай 2-5-р анги	Төлөвлөж буй
5	Төлөвлөж буй тоглоомын талбай 1-р анги	Төлөвлөж буй
6	Төлөвлөж буй тоглоомын талбай 6-9-р анги	Төлөвлөж буй
7	Төлөвлөж буй чийрэгжүүлэх талбай	Төлөвлөж буй
8	Төлөвлөж буй спортын талбай	Төлөвлөж буй

ЕРӨНХИЙ ТӨЛӨВЛӨГӨӨ М 1:500

ATA12937 9116621 9024070582

ЧИЙРЭГЖҮҮЛЭЛТИЙН ТАЛБАЙ 1800м2

ДУНД АНГИ 6-9 200м2

БАГА АНГИ 2-5 800м2

1-р АНГИ 1*7.2=360м2

DRY DECK FOUNTAIN

START

FINISH

Bicycle

Trash

ТАНИХ ТЭМДЭГЛЭГЭЭ

- Төлөвлөж буй барилга, байгууламж
- Төлөвлөж буй авто зам (2315м2)
- Төлөвлөж буй явган хүний зам (4344м2)
- Төлөвлөж буй дугуйн зам
- Төлөвлөж буй авто зогсоол (17 ширхэг)
- Төлөвлөж буй зүлэгжүүлсэн талбай (3810м2)
- Архитектур төлөвлөлтийн даалгаврын схемийн хил хязгаар
- Эзэмшил газрын хил хязгаар
- Одоо байгаа барилга
- Одоо байгаа нураах барилга байгууламж
- Одоо байгаа явган хүний зам
- Одоо байгаа орон нутгийн чанартай авто зам
- Бохир усны шугам
- Дулааны шугам
- Цэвэр усны шугам
- Цахилгааны шугам

1	Барилгын хэмжээ	56x79.2м	7	Галын гарц, аврах гарцын тоо	9ш
2	Барилгажих талбай	3673м2	8	Рамп, пандусын тоо — Машин ш/%	-
3	Хүчин чадал	640 хүүхэд		Рамп, пандусын тоо — ХБИ ш/%	6ш
4	Үйлчилгээний талбай	-	9	Сэргээгдэх эрчим хүч	-
5	Газар доорх авто зогсоол	-	10	Шинэ, шилдэг технологи	-
6	ХБИ-ий авто зогсоол	2ш	11	Архитектурын хэв маяг	Модерн

HYPOTENUSE DESIGN LLC
Барилгын зураг төслийн "ГИПОТЕНУЗ ДИЗАЙН" ХХК
УТАС : 88014798

640 ХҮҮХДИЙН СУРГУУЛИЙН БАРИЛГЫН НЭГ МАЯГИЙН ЗУРАГ ТӨСӨЛ	НЭР	ГАРЫН ҮСЭГ	ЗАГВАР ЗУРАГ
Гүйцэтгэгч: "Гипотенуз Дизайн" ХХК-н захирал	М.Энхтөр		М1:500
Гүйцэтгэгч: Архитектор	Б.Ариунзаяа		Хуудас-5
Захиалагч: Боловсролын яамны Санхүү, хөрөнгө оруулалтын хэлтсийн дарга	Х.Тамираа		2025 он

ХӨДӨЛГӨӨНИЙ СХЕМ М1:500

N

START 100м

START 400м

FINISH

ЧИЙРЭГЖҮҮЛЭЛТИЙН ТАЛБАЙ 1800м2

ДУНД АНГИ 6-9 200м2

Ц-р АНГИ 1*7.2=360м2

БАГА АНГИ
2-5 800м2

FINISH START

DRY DECK FOUNTAIN

Trash

Bicycle

56000

55000

7000

14000

3900

21000

700

36000

79500

13500

12000

3650

11500

15590

70°

20°

50000

56413

6413

19000

2100

20000

2100

А Е Ж К

Д' Ж' Х1 Х9 Х10 У1 У3 У4

1 2 3 4 5 11 12 15 16

Автомашины хөдөлгөөн

Онцгой үед галын машин зорчих зам

Явган зорчигчийн хөдөлгөөн

ТОДОРХОЙЛОЛТ

№	Нэр	Хүчин чадал/м2	Урт/м
1	Төлөвлөж буй авто зам, зогсоол	2315м2	298м
2	Төлөвлөж буй явган хүний зам	4344м2	м
3	Төлөвлөж буй хүүхдийн тоглоомын талбайн зориулалтын EPDM резинэн шал	5760м2	м
4	Төлөвлөж буй хөлбөмбөгийн талбай	6438м2	100.6м

Барилгын зураг төслийн "ГИПОТЕНУЗ ДИЗАЙН" ХХК

УТАС : 88014798

640 ХҮҮХДИЙН СУРГУУЛИЙН БАРИЛГЫН НЭГ МАЯГИЙН ЗУРАГ ТӨСӨЛ	НЭР	ГАРЫН ҮСЭГ	ЗАГВАР ЗУРАГ
Гүйцэтгэгч: "Гипотенуз Дизайн" ХХК-н захирал	М.Энхтөр		М1:500
Гүйцэтгэгч: Архитектор	Б.Ариунзаяа		Хуудас-6
Захиалагч: Боловсролын яамны Санхүү, хөрөнгө оруулалтын хэлтсийн дарга	Х.Тамираа		2025 он

ТОХИЖИЛТ НОГООН БАЙГУУЛАМЖ-1 М1:500

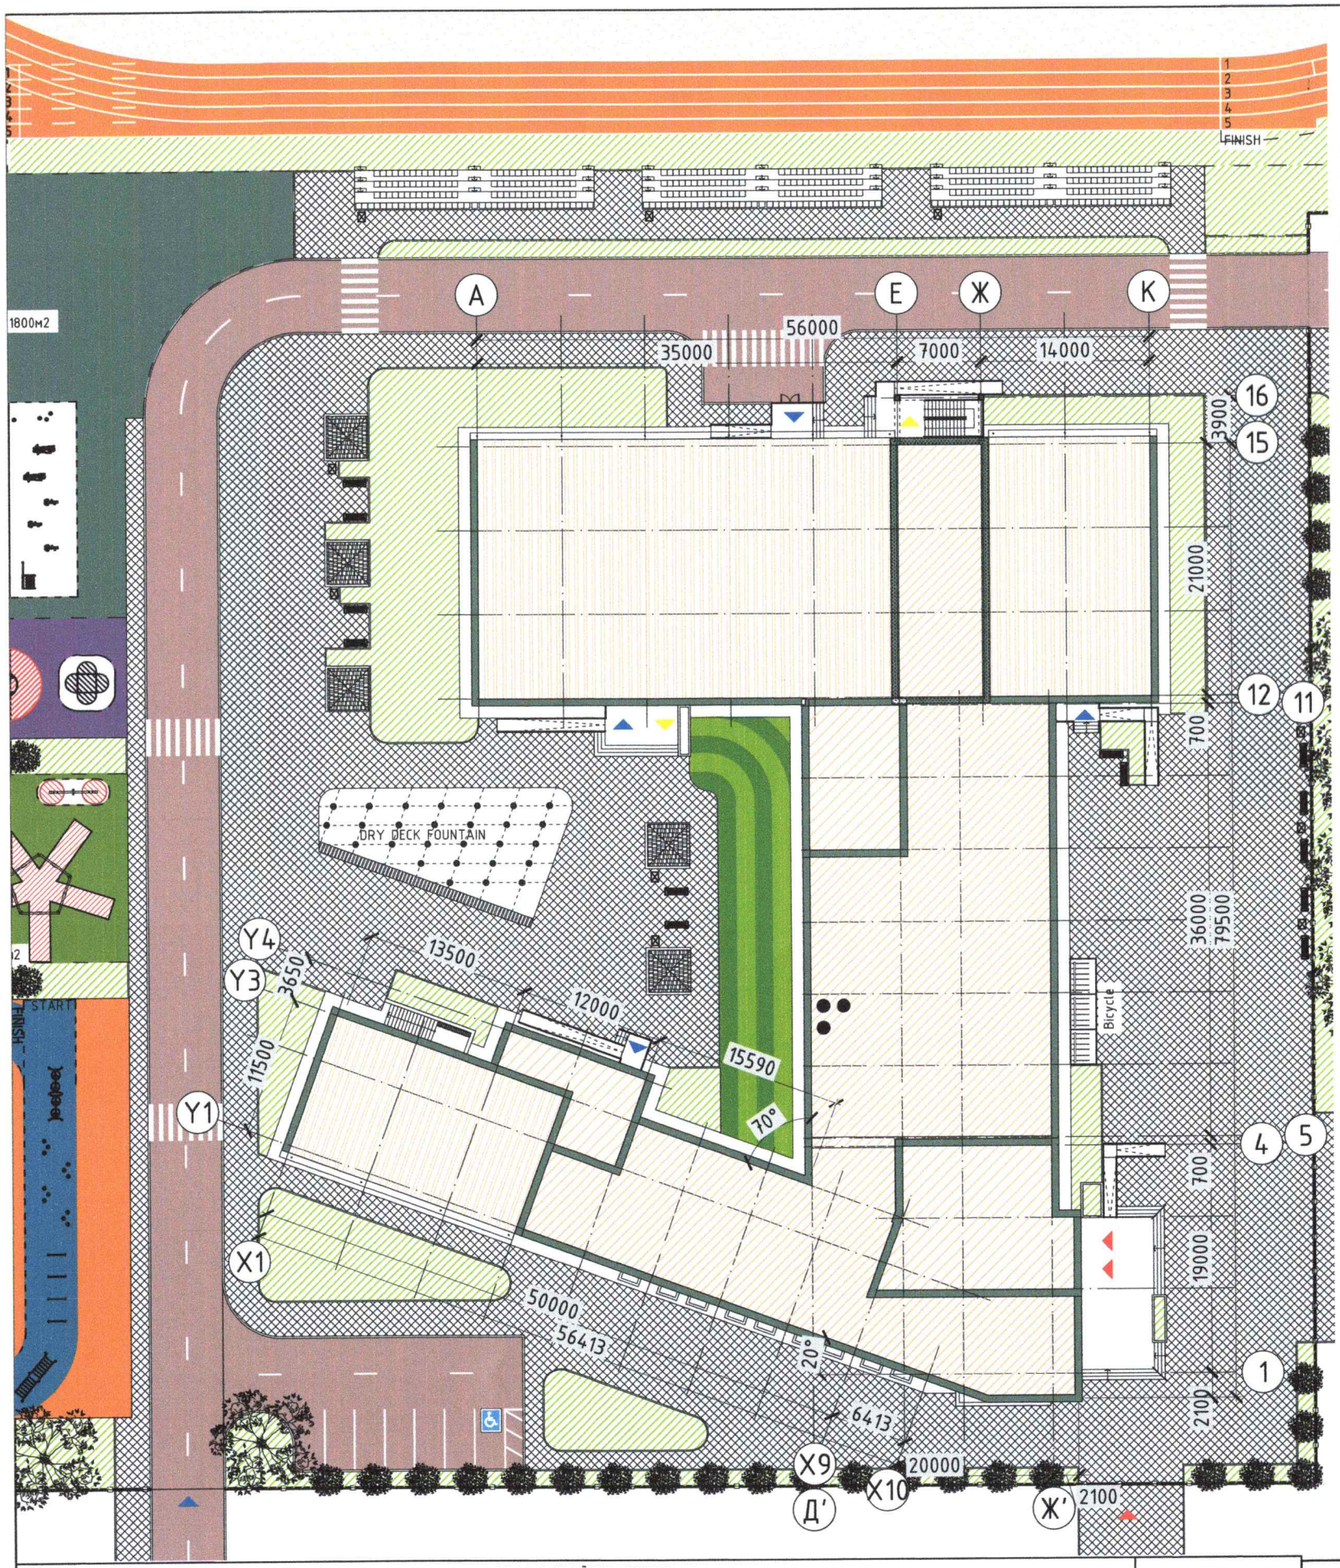

ГАДНА ТОХИЖИЛТОНД ДАРААХ ТОНОГЛОЛУУДЫГ ДҮЙЦҮҮЛЭН СОНГОНО. / ЖИШЭЭ ЗУРАГ/

Хогийн сав

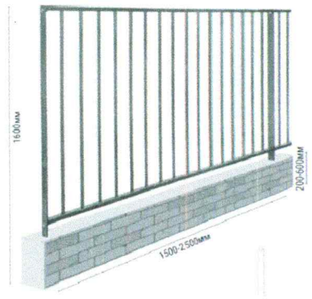

Эдэлбэр газрын хашаа

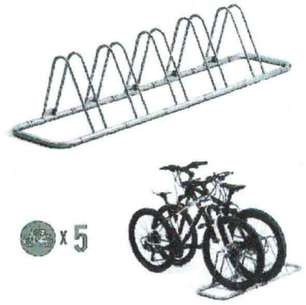

Унадаг дугуйн зогсоол /төмөр, ган/

Явган хүний сандал

Зам талбайн гадна гэрэлтүүлэг /Шонгийн өнгө: ган мөнгөлөг, нерж

Модон сүүдрэвч

ТАНИХ ТЭМДЭГЛЭГЭЭ

- Эдэлбэр газрын хашаа
- Төлөвлөж буй хайрган хучилттай талбай
- Төлөвлөж буй зүлгэн талбай /3810+3970м2/
- Төлөвлөж буй мод ургамалан хайс
- Явган хүний сандал
- Зам талбайн гадна гэрэлтүүлэг
- Хогийн сав
- Дугуйн зогсоол

Тохижилтын тоноглол:
Явган хүний сандал- 16+370ш
Гадна гэрэлтүүлэг-
Хогийн сав- 16ш
Дугуйн зогсоол-15ш

Авто зогсоол:
Ээмшлийн гадна зогсоол -7ш
Ээмшлийн дотор зогсоол -10
Хөгжлийн бэрхшээлтэй иргэний гадна зогсоол-2ш

Тайлбар:
Гадна тохижилтонд дараах "Нийслэлийн хэмжээнд мөрдүүлэх стандарт, шаардлага"-уудыг тус тус мөрдсөн байна.

- UCS0001-02-2019 Хашаа, хайс, хашлаганд тавигдах ерөнхий шаардлага,хэрэглээ
- UCS1901B-2020 Гэрэлтүүлэг,гэрлэн чимэглэл
- UCS1403C-2020 Нийтийн ээмшлийн гудамж зам талбайд байршуулах хогны савны тавигдах шаардлага
- UCS1404C-2020 Нийтийн ээмшлийн гудамж талбайд байршуулах сандалд тавигдах шаардлага
- UCS0903B-2020 Унадаг дугуйн замын төлөвлөд,хучилтанд тавигдах шаардлага
- UCS0002-02:2019 Хүүхдийн тоглоомын талбайн эрүүл, аюулгүй орчныг бүрдүүлэхэд тавигдах ерөнхий шаардлага

НОГООН БАЙГУУЛАМЖ

Ногоон байгууламжийн ангилал	МОДНЫ ТӨРӨЛ /ТОО Ш./	БУТ СӨӨГНИЙ ТӨРӨЛ / ТОО ШИРХЭГ/	ЗҮЛЭГЖҮҮЛЭЛТ /М2/	СПОРТ ТАЛБАЙ /М2/	НОГООН БАЙГУУЛАМЖИЙН ЭЗЛЭХ ХУВЬ
Нийтийн хэрэгцээний ногоон байгууламж	0	0	0	0	0
Хязгаарлагдмал хэрэгцээний ногоон байгууламж	15	60	3810м2	6438м2	11+22%
Тусгай зориулалтын ногоон байгууламж	0	0	0	0	0
Нийт	15	60	3810м2	6438м2	11+22%

	640 ХҮҮХДИЙН СУРГУУЛИЙН БАРИЛГЫН НЭГ МАЯГИЙН ЗУРАГ ТӨСӨЛ	НЭР	ГАРЫН ҮСЭГ	ЗАГВАР ЗУРАГ
Гипотенуз Дизайн ХХК Барилгын зураг төслийн "ГИПОТЕНУЗ ДИЗАЙН" ХХК	Гүйцэтгэгч: "Гипотенуз Дизайн" ХХК-н захирал	М.Энхтөр		М1:500
УТАС : 88014798	Гүйцэтгэгч: Архитектор	Б.Ариунзаяа		Хуудас-7
	Захиалагч: Боловсролын яамны Санхүү, хөрөнгө оруулалтын хэлтсийн дарга	Х.Тамираа		2025 он

СУРГУУЛИЙН ГАДНА ТАЛБАЙН ХАРАГДАХ БАЙДАЛ

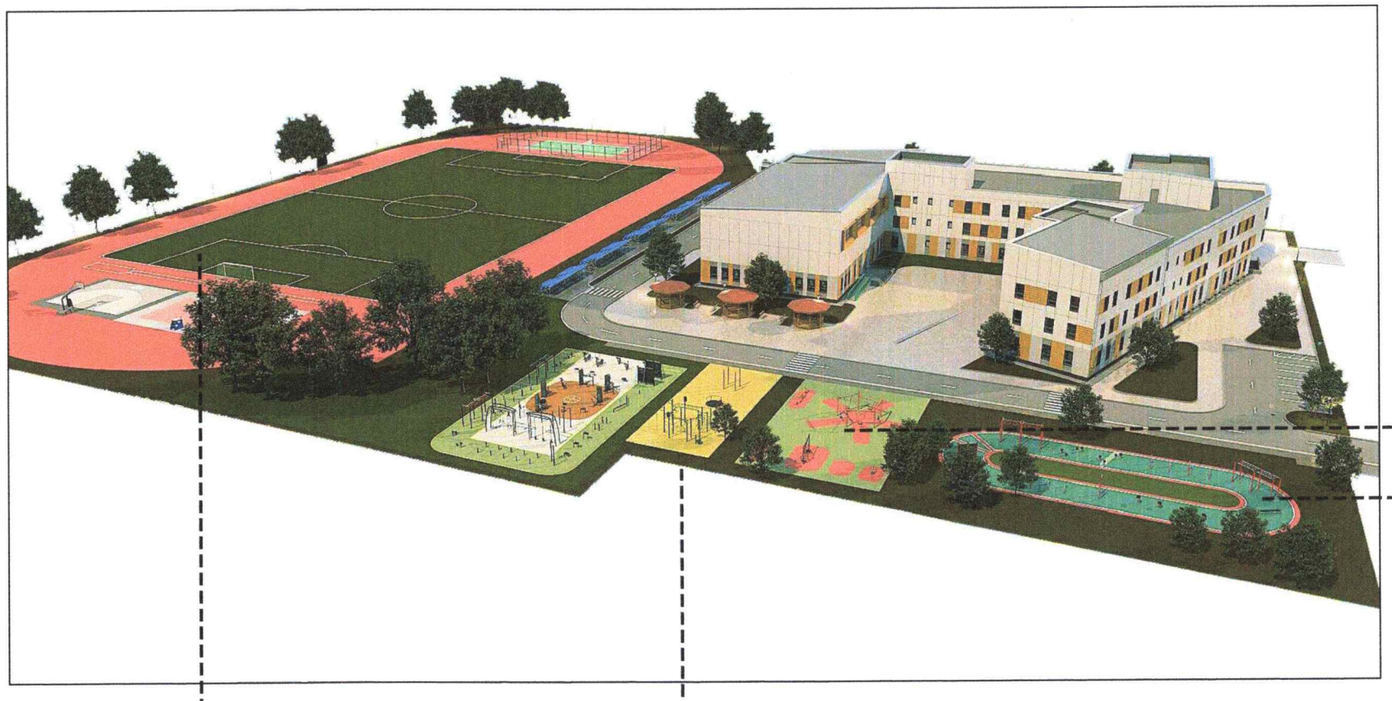

ТОХИЖИЛТ НОГООН БАЙГУУЛАМЖ-2 М1:500

1-р ангийн хүүхдийн тоглоомын талбай

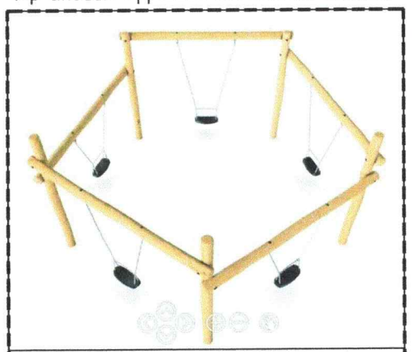

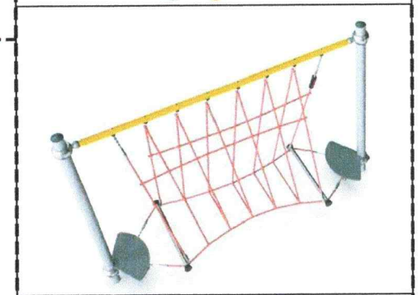

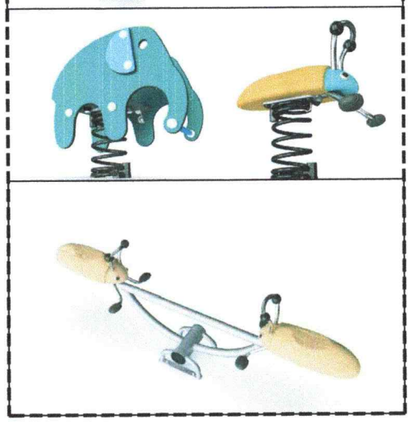

2-5-р ангийн хүүхдийн тоглоомын талбай

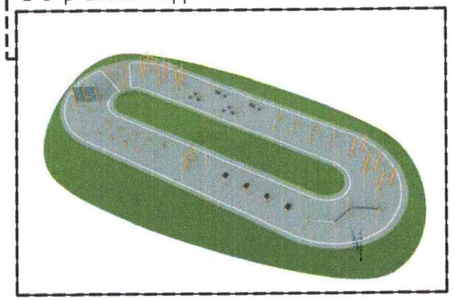

6-9-р ангийн хүүхдийн тоглоомын талбай

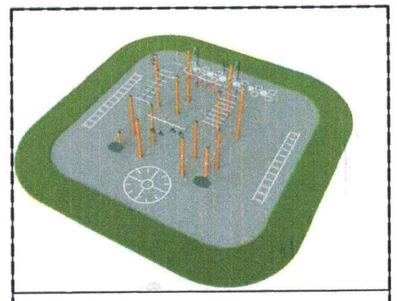

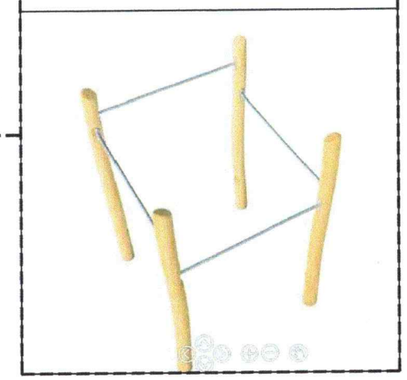

Гадна спорт хөл бөмбөгийн талбай

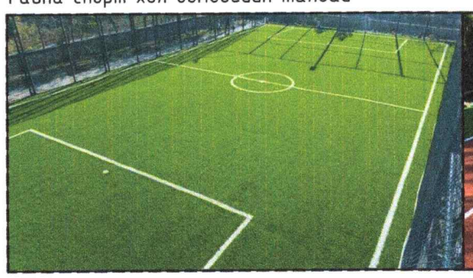

Гадна спорт гүйлтийн зам

Гадна спорт одон бөмбөгийн талбай

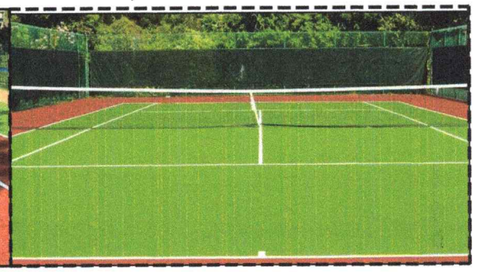

Гадна спорт гар бөмбөгийн талбай

Гадна спорт 3х3 сагсан бөмбөгийн талбай

UCS0002-02:2019 Хүүхдийн тоглоомын талбайн эрүүл, аюулгүй орчныг бүрдүүлэхэд тавигдах ерөнхий шаардлагад нийцэх тоглоомыг сонгож, дээрх жишээ зургийн дагуу дүйцүүлнэ.

Барилгын зураг төслийн "ГИПОТЕНУЗ ДИЗАЙН" ХХК	640 ХҮҮХДИЙН СУРГУУЛИЙН БАРИЛГЫН НЭГ МАЯГИЙН ЗУРАГ ТӨСӨЛ	НЭР	ГАРЫН ҮСЭГ	ЗАГВАР ЗУРАГ
	Гүйцэтгэгч: "Гипотенуз Дизайн" ХХК-н захирал	М.Энхтөр		М1:500
	Гүйцэтгэгч: Архитектор	Б.Ариунзаяа		Хуудас-8
УТАС : 88014798	Захиалагч: Боловсролын яамны Санхүү, хөрөнгө оруулалтын хэлтсийн дарга	Х.Тамираа		2025 он

ХАРАГДАХ БАЙДАЛ

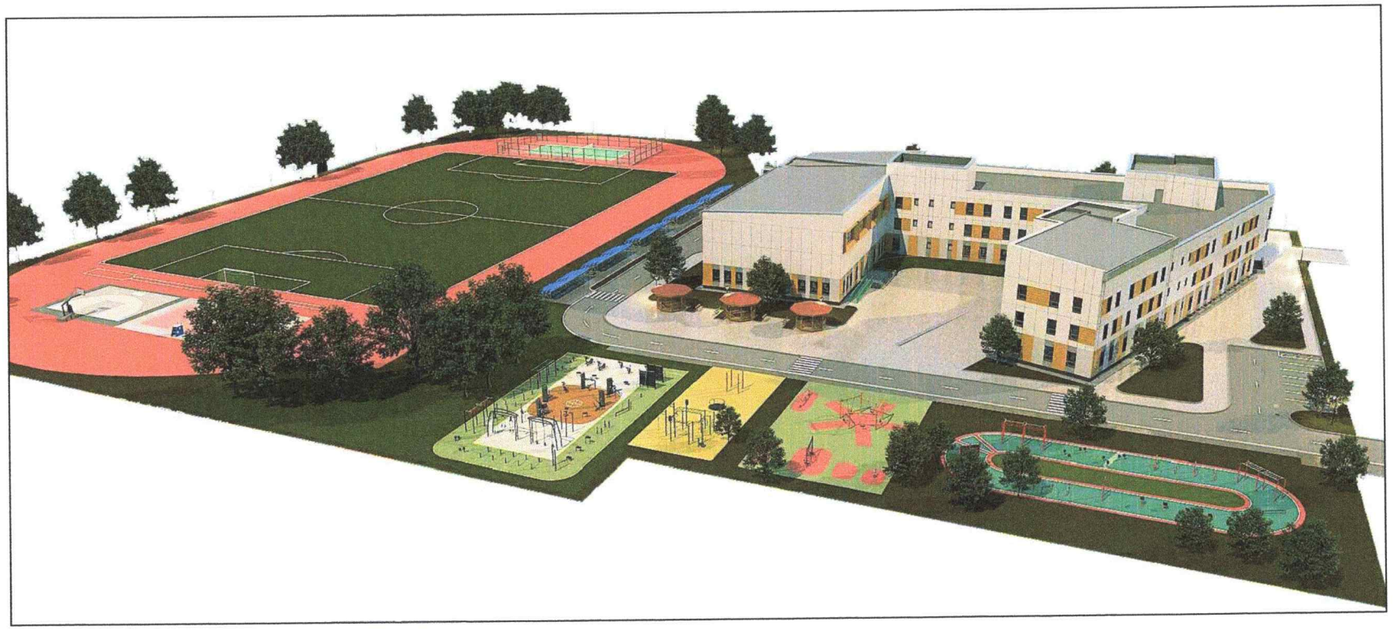

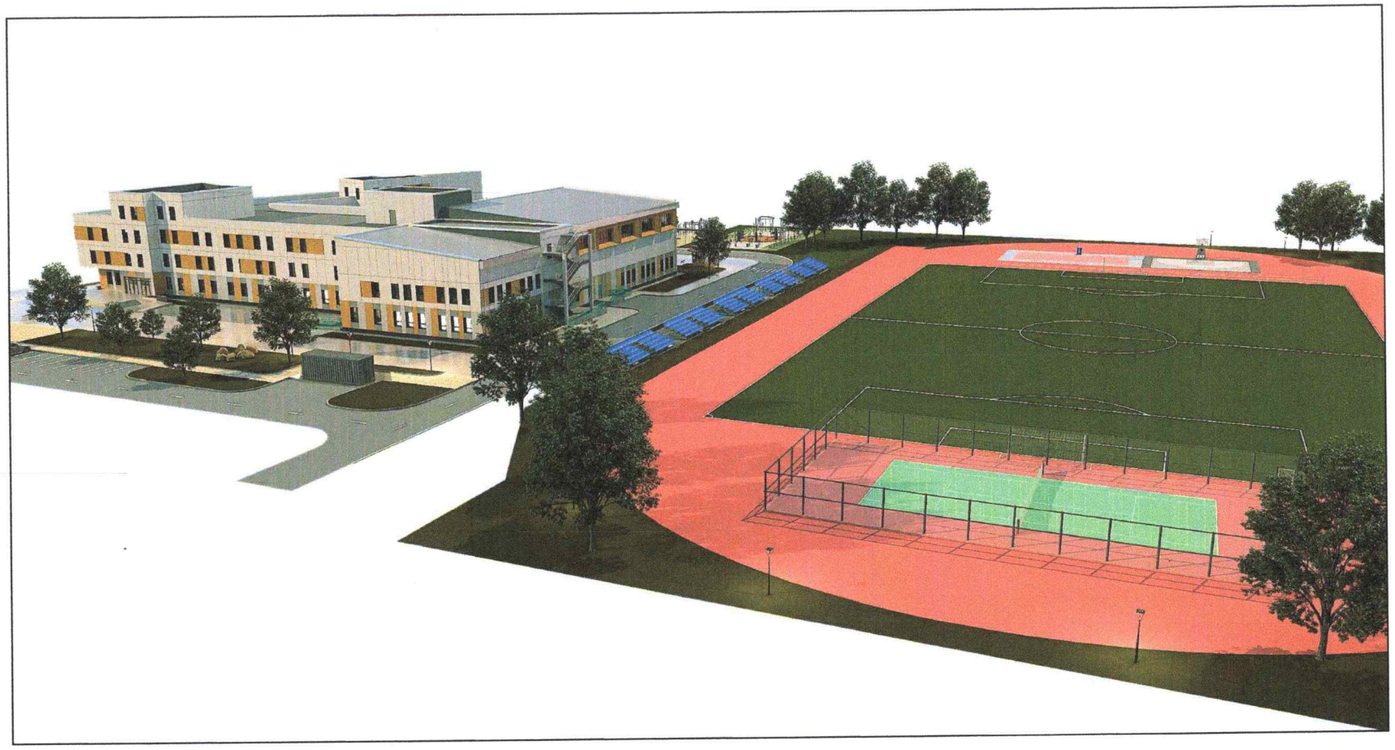

Mongolian Design LLC Барилгын зураг төслийн "ГИПОТЕНУЗ ДИЗАЙН" ХХК УТАС : 88014798	640 ХҮҮХДИЙН СУРГУУЛИЙН БАРИЛГЫН НЭГ МАЯГИЙН ЗУРАГ ТӨСӨЛ	НЭР	ГАРЫН ҮСЭГ	ЗАГВАР ЗУРАГ
	Гүйцэтгэгч: "Гипотенуз Дизайн" ХХК-н захирал	М.Энхтөр		М1:---
	Гүйцэтгэгч: Архитектор	Б.Ариунзаяа		Хуудас-9
	Захиалагч: Боловсролын яамны Санхүү, хөрөнгө оруулалтын хэлтсийн дарга	Х.Тамираа		2025 он

Зоорийн давхар галын гарцны схем М1:400

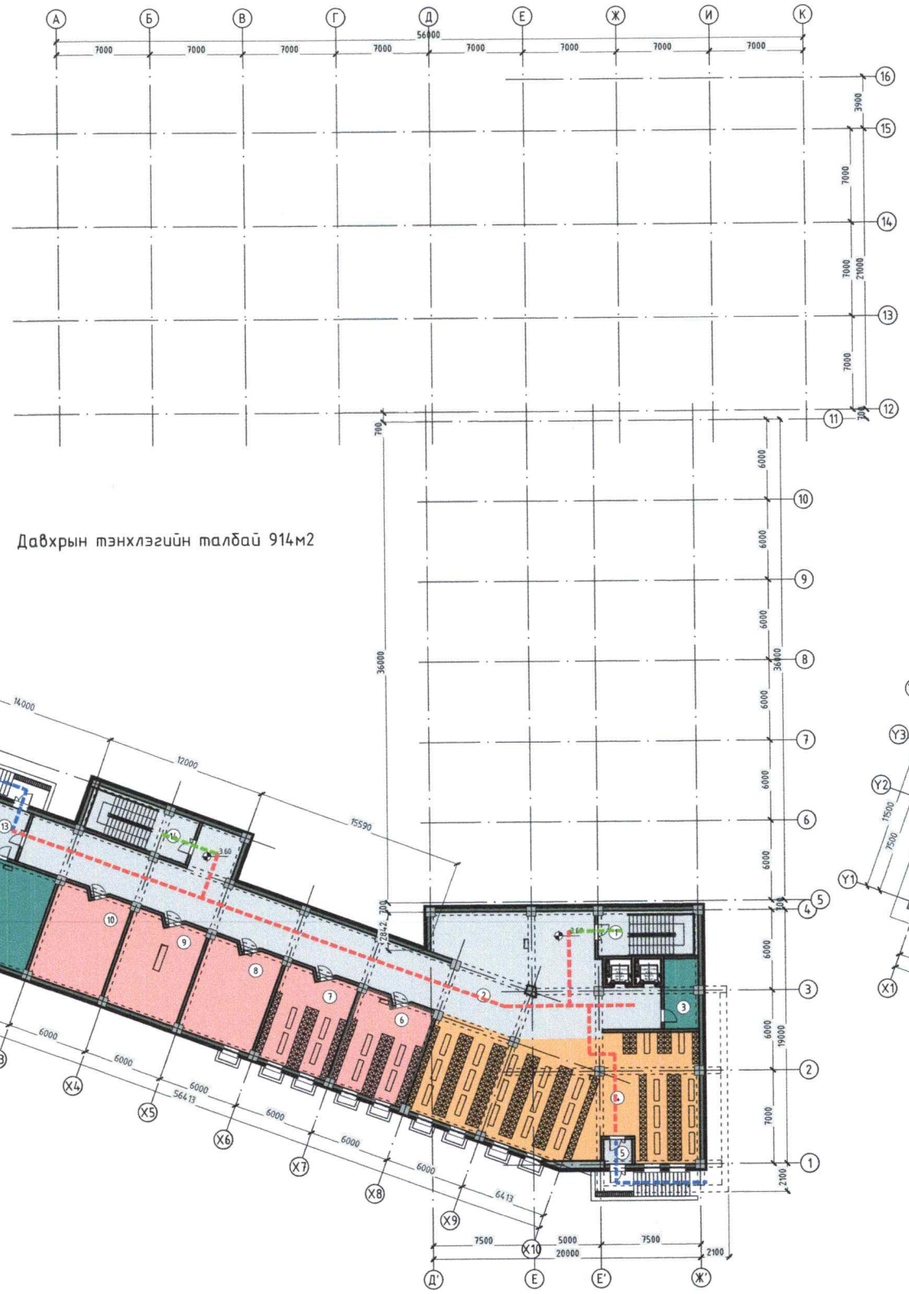

1-р давхар галын гарцны схем М1:400

Гадагш гарах гарц

зорчих хэсэг /коридор/

Шатны хонгил

Barilgiin zurag tsleeiin "ГИПОТЕНУЗ ДИЗАЙН" ХХК	640 ХҮҮХДИЙН СУРГУУЛИЙН БАРИЛГЫН НЭГ МАЯГИЙН ЗУРАГ ТӨСӨЛ	НЭР	ГАРЫН ҮСЭГ	ЗАГВАР ЗУРАГ
УТАС : 88014798	Гүйцэтгэгч: "Гипотенуз Дизайн" ХХК-н захирал	М.Энхтөр		М1:400
	Гүйцэтгэгч: Архитектор	Б.Ариунзаяа		Хуудас-15
	Захиалагч: Боловсролын яамны Санхүү, хөрөнгө оруулалтын хэлтсийн дарга	Х.Тамираа		2025 он

ЗООРИЙН ДАВХРЫН БАЙГУУЛАЛТ М1:200

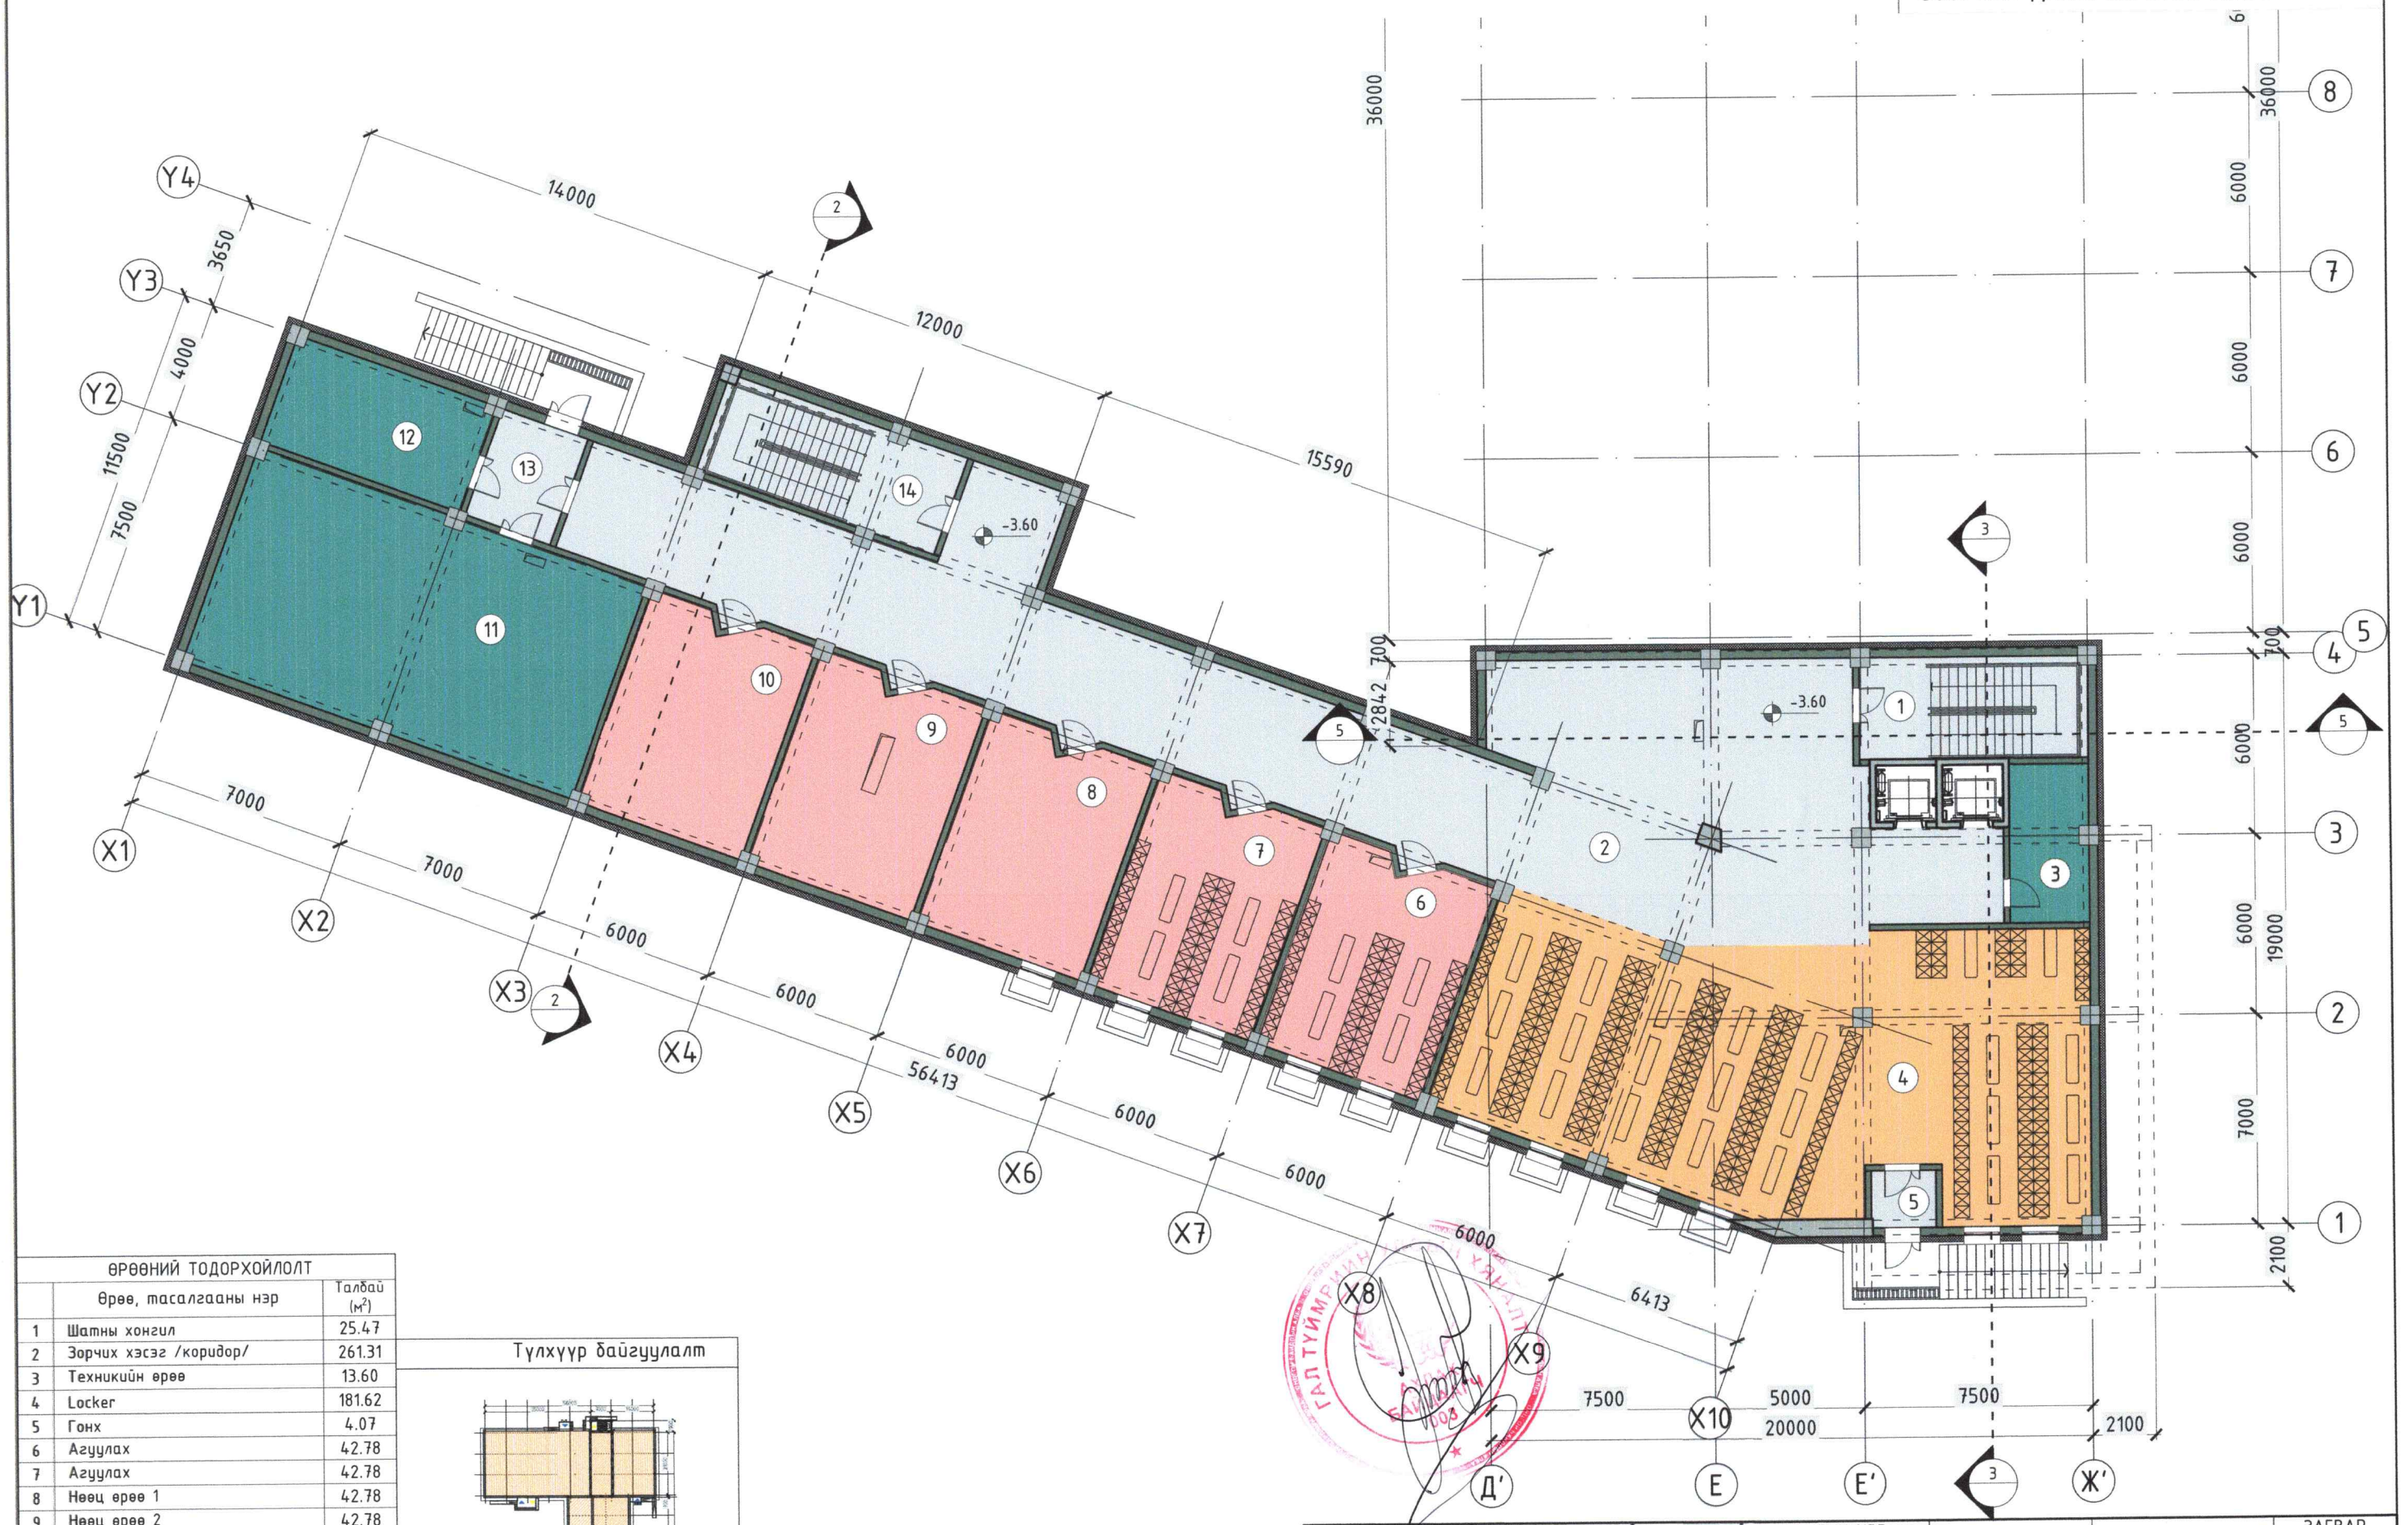

ӨРӨӨНИЙ ТОДОРХОЙЛОЛТ		
	Өрөө, тасалгааны нэр	Талбай ($м^2$)
1	Шатны хонгил	25.47
2	Зорчих хэсэг /коридор/	261.31
3	Техникийн өрөө	13.60
4	Locker	181.62
5	Гонх	4.07
6	Агуулах	42.78
7	Агуулах	42.78
8	Нөөц өрөө 1	42.78
9	Нөөц өрөө 2	42.78
10	Нөөц өрөө 2	42.78
11	Техникийн өрөө	103.20
12	Техникийн өрөө	26.21
13	Гонх	11.23
14	Шатны хонгил	28.25
	Нийт талбай	868.87
	Тэнхлэгийн талбай	914.33

Түлхүүр байгуулалт

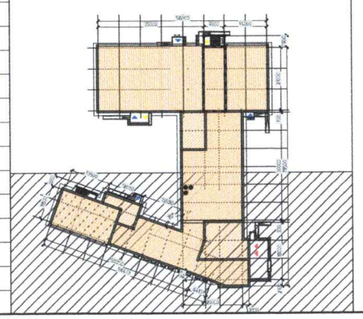

Гипотенуз Дизайн ХХК Барилгын зураг төслийн "ГИПОТЕНУЗ ДИЗАЙН" ХХК УТАС : 88014798	640 ХҮҮХДИЙН СУРГУУЛИЙН БАРИЛГЫН НЭГ МАЯГИЙН ЗУРАГ ТӨСӨЛ	НЭР	ГАРЫН ҮСЭГ	ЗАГВАР ЗУРАГ
	Гүйцэтгэгч: "Гипотенуз Дизайн" ХХК-н захирал	М.Энхтөр		М1:200
	Гүйцэтгэгч: Архитектор	Б.Ариунзаяа		Хуудас-11
	Захиалагч: Боловсролын яамны Санхүү, хөрөнгө оруулалтын хэлтсийн дарга	Х.Тамираа		2025 он

1-р ДАВХРЫН БАЙГУУЛАЛТ М1:200

ӨРӨӨНИЙ ТОДОРХОЙЛОЛТ		
	Өрөө, тасалгааны нэр	Талбай ($м^2$)
1	Гол орц	12.82
2	Үүдний танхим	178.02
3	Зочдын өлгүүр	18.17
4	Бага булгийн өдөр өнжүүлэх	75.66
5	1-5-р анги хич.танхим	78.32
6	АЦӨ Я.Х.Х	5.26
7	Бага булгийн АЦӨ эм	12.87
8	АЦӨ эм	9.31
9	Бага булгийн АЦӨ эр	13.80
10	1-5-р анги хич.танхим	75.94
11	Амралтын өрөө	18.27
12	1-5-р анги хич.танхим	76.63
13	Шатны хонгил	28.24
14	Зорчих хэсэг /коридор/	227.56
15	Шатны хонгил	22.03
16	1-5-р анги хич.танхим	76.10
17	Ганцаарчилсан сургалтын өрөө	22.80
18	1-5-р анги хич.танхим	75.28
19	1-5-р анги хич.танхим	75.60

Түлхүүр байгууламт

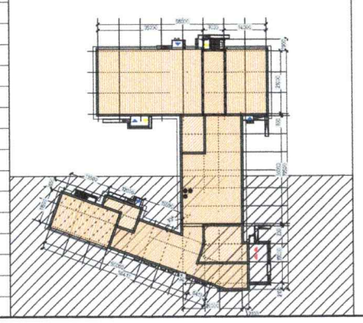

Hypotenuse Design LLC Барилгын зураг төслийн "ГИПОТЕНУЗ ДИЗАЙН" ХХК	640 ХҮҮХДИЙН СУРГУУЛИЙН БАРИЛГЫН НЭГ МАЯГИЙН ЗУРАГ ТӨСӨЛ	НЭР	ГАРЫН ҮСЭГ	ЗАГВАР ЗУРАГ
УТАС : 88014798	Гүйцэтгэгч: "Гипотенуз Дизайн" ХХК-н захирал	М.Энхтөр		М1:200
	Гүйцэтгэгч: Архитектор	Б.Ариунзаяа		Хуудас-13
	Захиалагч: Боловсролын яамны Санхүү, хөрөнгө оруулалтын хэлтсийн дарга	Х.Тамираа		2025 он

1-р ДАВХРЫН БАЙГУУЛАЛТ М1:200

ӨРӨӨНИЙ ТОДОРХОЙЛОЛТ

	Өрөө, тасалгааны нэр	Талбай (м²)
20	1-5-р анги хич.танхим	75.20
21	Хурлын өрөө	38.11
22	1-5-р анги хич.танхим	75.12
23	Бага бүлгийн АЦӨ эр	13.80
24	Бага бүлгийн АЦӨ эм	13.46
25	АЦӨ эр	8.38
26	АЦӨ Я.Х.Х	5.25
27	Шатны хонгил	23.71
28	Зорчих хэсэг /коридор/	209.23
29	Зорчих хэсэг /коридор/	211.98
30	Цэвэрлэгээний тоног төхөөрөмж хадгалах өрөө	6.50
31	АЦӨ эр	12.22
32	АЦӨ эм	9.17
33	Сэтгэлзүйчийн өрөө	17.28
34	Хоолзүйчийн өрөө	12.75
35	Хооллох заал	174.40
36	Хоол түгээлтийн хэсэг	17.96
37	Халуун цех	47.39
38	Аяга таваг угаалга	30.27
39	Хог түр хадгалах өрөө	8.08
40	Х.Ц Бэлтгэлийн хэсгүүд	71.76
41	Х.Ц хувцас солих өрөө	28.52
42	Ногооны агуулах	13.27
43	Хүүрай хүнсний агуулах	10.47
44	Хөргүүртэй агуулах	5.46
45	Хүйтэн агуулах	6.02
46	Сүүн бүтээгдэхүүний агуулах	6.02
47	Номын сан /фонд/	26.68
48	Ном засварлах хэсэг	8.18
49	Уншлагын танхим	153.90
50	Технологи, Хөдөлмөрийн хичээлийн танхим /эм/	72.06
51	Технологи, Хөдөлмөрийн хичээлийн танхим /эр/	72.06
52	Гонх	7.23
53	Тусгаарлах өрөө	10.04
54	Эмчийн өрөө	16.45
55	Цэвэрлэгээний тоног төхөөрөмж хадгалах өрөө	8.40
	Нийт талбай	2629.46
	Тэнхлэгийн талбай	2850.93

Түлхүүр байгууламт

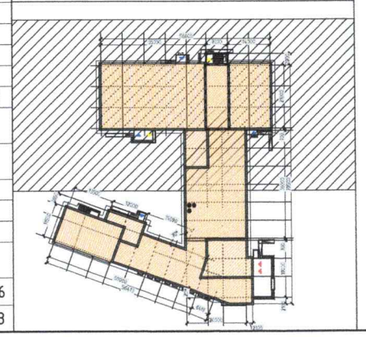

ГАЛ ТҮЙМРИЙН ХЯНАЛТ

HYPOTENUSE DESIGN LLC Баригдын зураг төслийн "ГИПОТЕНУЗ ДИЗАЙН" ХХК	640 ХҮҮХДИЙН СУРГУУЛИЙН БАРИЛГЫН НЭГ МАЯГИЙН ЗУРАГ ТӨСӨЛ	НЭР	ГАРЫН ҮСЭГ	ЗАГВАР ЗУРАГ
	Гүйцэтгэгч: "Гипотенуз Дизайн" ХХК-н захирал	М.Энхтөр		М1:200
	Гүйцэтгэгч: Архитектор	Б.Ариунзаяа		Хуудас-14
УТАС : 88014798	Захиалагч: Боловсролын яамны Санхүү, хөрөнгө оруулалтын хэлтсийн дарга	Х.Тамираа		2025 он

2-р давхар галын гарцны схем М1:400

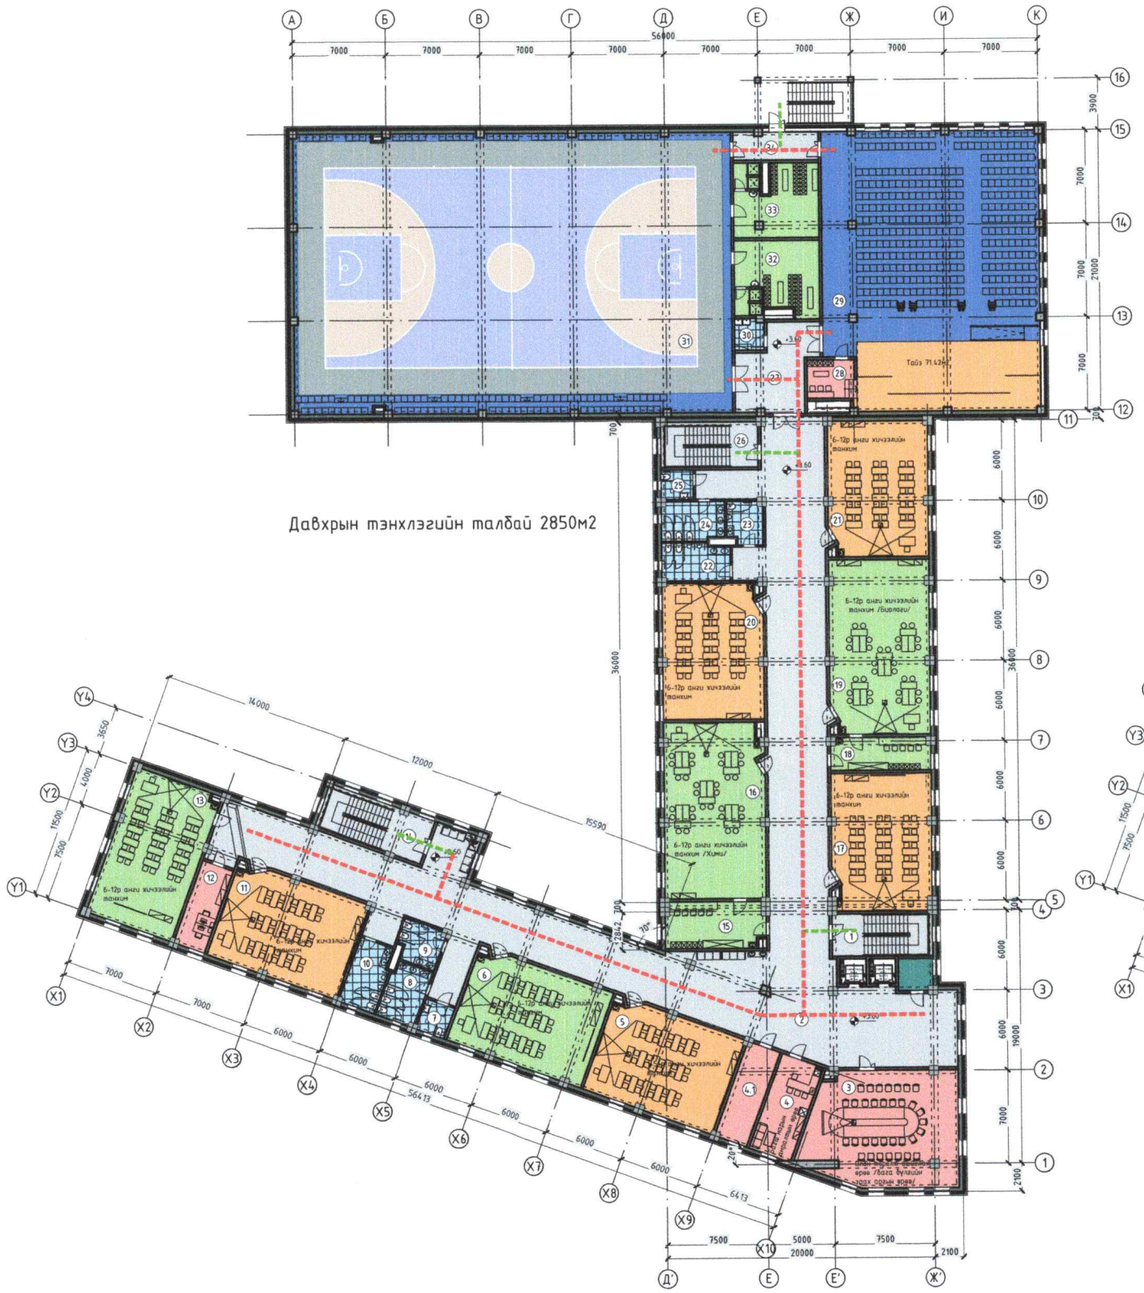
А Б В Г Д Е Ж И К
7000 7000 7000 7000 56000 7000 7000 7000 7000
16 15 14 13 12 11 10 9 8 7 6 5 4 3 2 1
3900 7000 7000 21000 7000 7000 6000 6000 6

2-р ДАВХРЫН БАЙГУУЛАЛТ М1:200

ӨРӨӨНИЙ ТОДОРХОЙЛОЛТ		
	Өрөө, тасалгааны нэр	Талбай ($м^2$)
1	Шатны хонгил	23.75
2	Зорчих хэсэг /коридор/	504.88
3	Олон төрөлт ашиглах өрөө /бага бүлгийн заах аргын өрөө/	93.60
4	Багш нарийн амралтын өрөө	24.59
4.1	Хувцасны өлгүүр	18.93
5	1-5-р анги хичээлийн танхим	75.66
6	6-12-р анги хичээлийн танхим	78.32
7	АЦӨ Я.Х.Х	5.26
8	Дунд ахлах бүлгийн АЦӨ эм	12.87
9	АЦӨ эм	9.31
10	Дунд ахлах бүлгийн АЦӨ эр	13.80
11	6-12-р анги хичээлийн танхим	75.94
12	Багш нарийн өрөө	15.94
13	6-12-р анги хичээлийн танхим	76.63
14	Шатны хонгил	28.24
15	Хими хичээлийн Лаборатори	25.11
16	6-12-р анги хичээлийн танхим /хими/	97.52
17	6-12-р анги хичээлийн танхим	75.72
18	Биологи хичээлийн Лаборатори	18.49
	6-12-р анги хичээлийн танхим	

Түлхүүр байгууламт

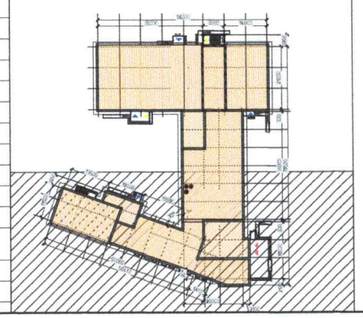

Барилгын зураг төслийн "ГИПОТЕНУЗ ДИЗАЙН" ХХК	640 ХҮҮХДИЙН СУРГУУЛИЙН БАРИЛГЫН НЭГ МАЯГИЙН ЗУРАГ ТӨСӨЛ	НЭР	ГАРЫН ҮСЭГ	ЗАГВАР ЗУРАГ
УТАС : 88014798	Гүйцэтгэгч: "Гипотенуз Дизайн" ХХК-н захирал	М.Энхтөр		М1:200
	Гүйцэтгэгч: Архитектор	Б.Ариунзаяа		Хуудас-16
	Захиалагч: Боловсролын яамны Санхүү, хөрөнгө оруулалтын хэлтсийн дарга	Х.Тамираа		2025 он

2-р ДАВХРЫН БАЙГУУЛАЛТ М1:200

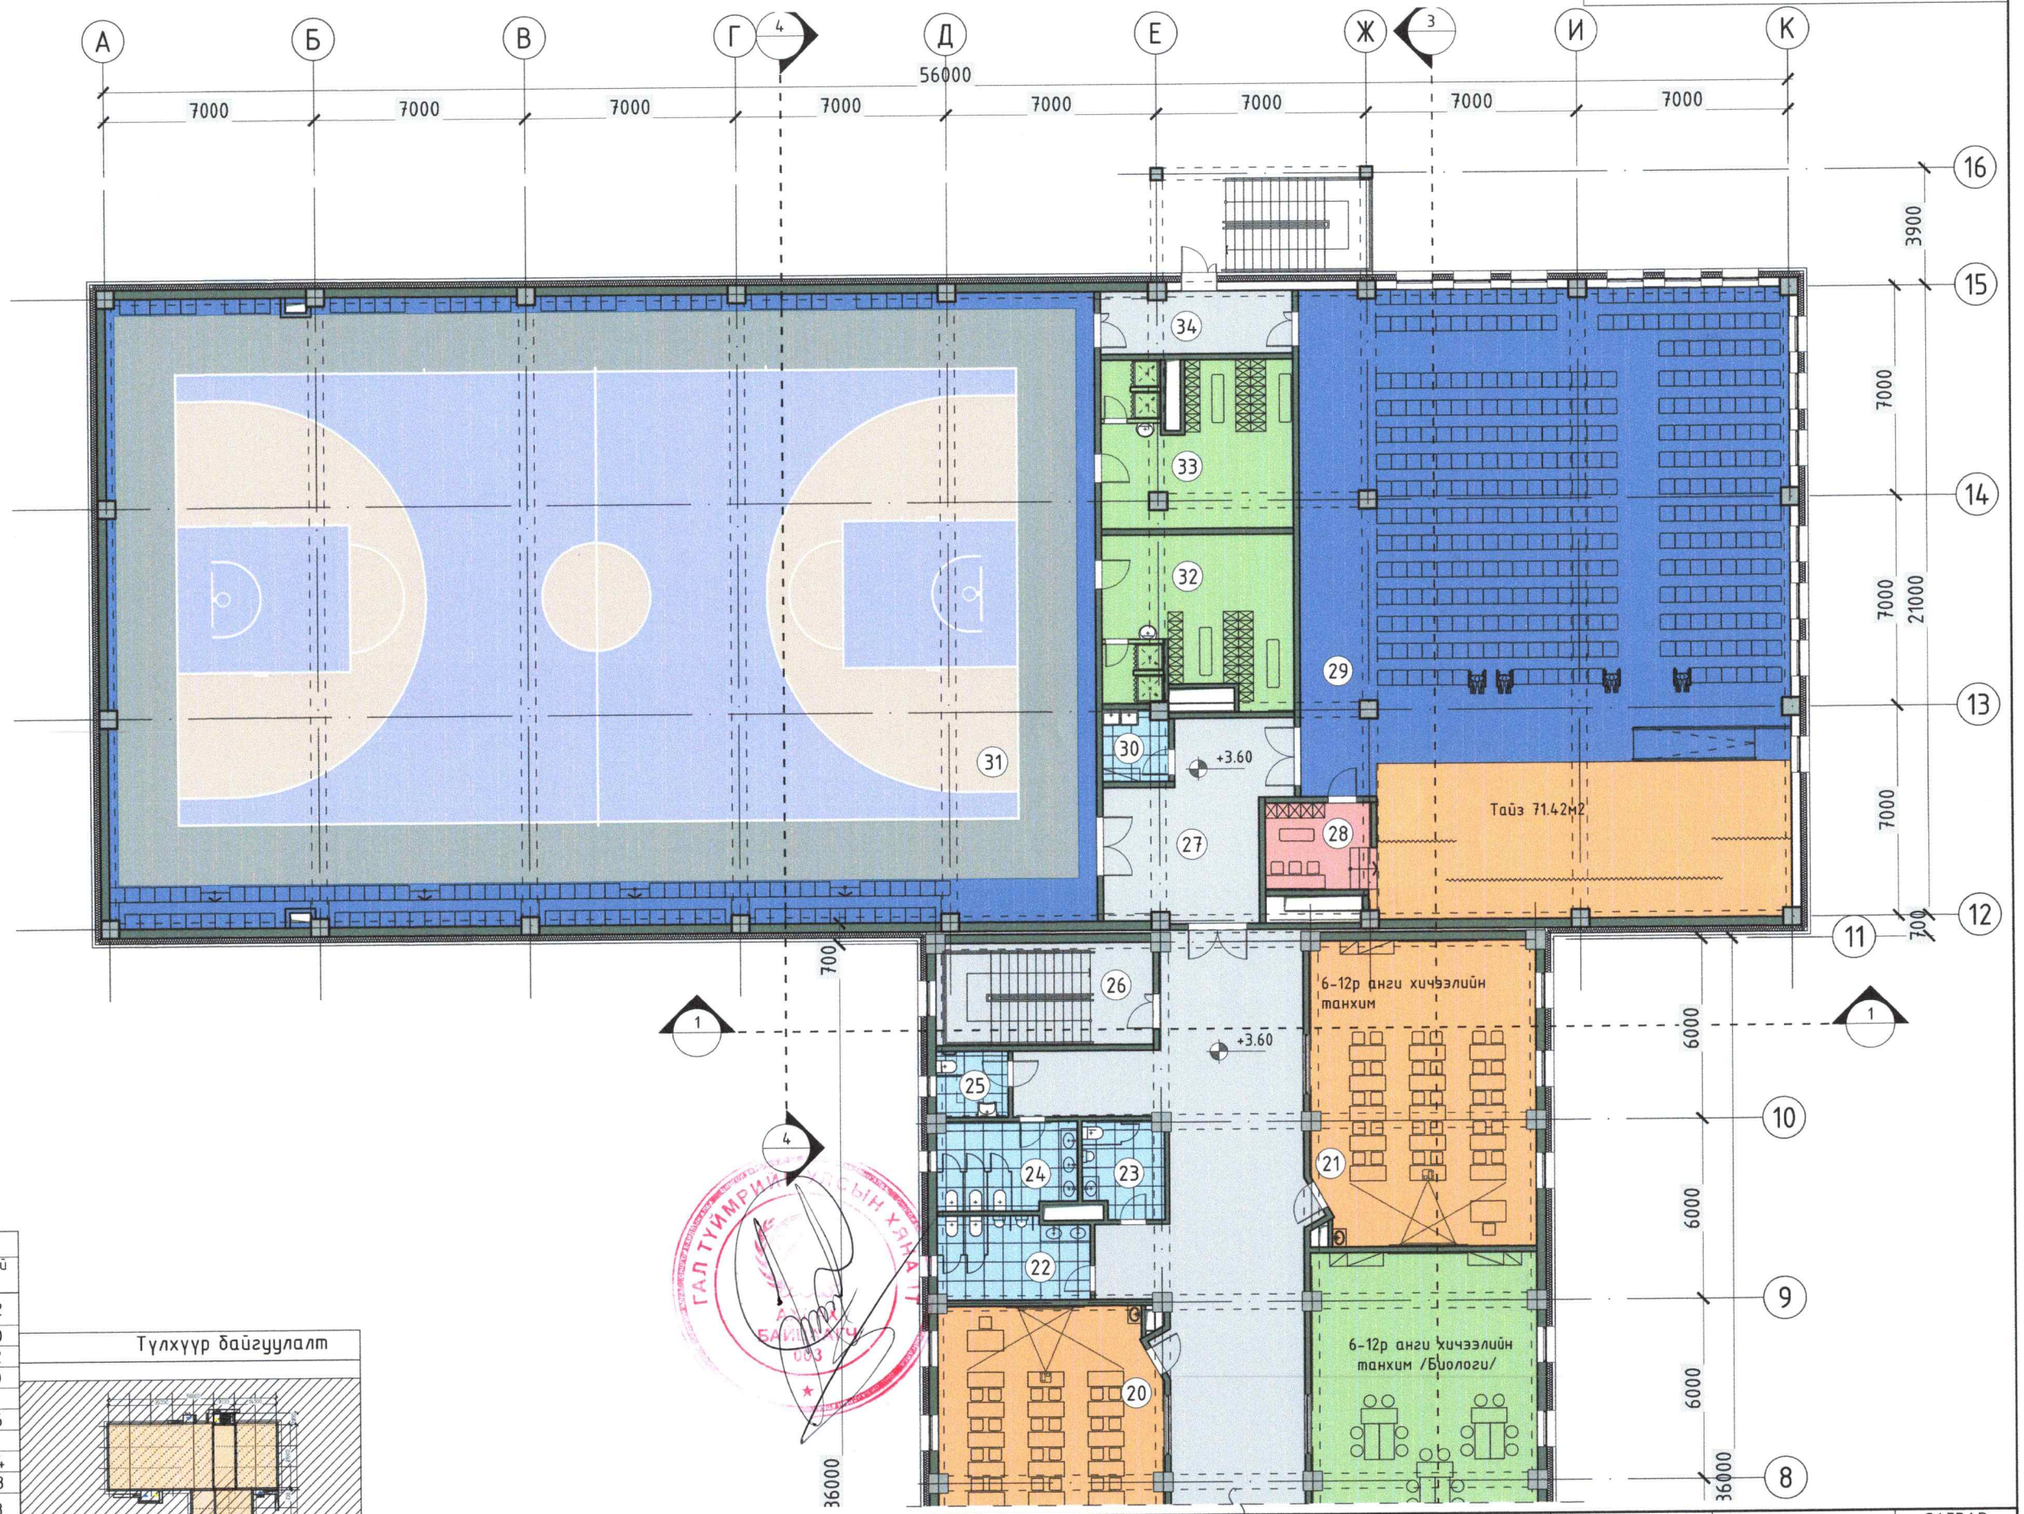

ӨРӨӨНИЙ ТОДОРХОЙЛОЛТ		
	Өрөө, тасалгааны нэр	Талбай ($м^2$)
19	6-12-р анги хичээлийн танхим /биологи/	96.82
20	6-12-р анги хичээлийн танхим	75.20
21	6-12-р анги хичээлийн танхим	75.12
22	Дунд ахлах булгийн АЦӨ эр	13.80
23	АЦӨ эм	8.38
24	Дунд ахлах булгийн АЦӨ эм	13.46
25	АЦӨ Я.Х.Х	5.25
26	Шатны хонгил	24.54
27	Зорчих хэсэг /коридор/	32.88
28	Хубцас солих өрөө /Урлаг танхим/	10.58
29	Урлаг танхим	330.77
30	Цэвэрлэгээний тоног төхөөрөмж хадгалах өрөө	5.07
31	Спорт заал 1	688.92
32	Хубцас солих өрөө	34.71
33	Хубцас солих өрөө	34.00
34	Зугтах гарцын гонх	13.26
	Нийт талбай	2737.32

Түлхүүр байгууламт

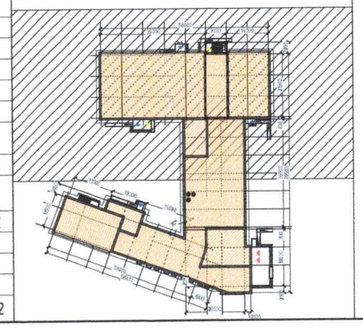

	640 ХҮҮХДИЙН СУРГУУЛИЙН БАРИЛГЫН НЭГ МАЯГИЙН ЗУРАГ ТӨСӨЛ	НЭР	ГАРЫН ҮСЭГ	ЗАГВАР ЗУРАГ
Гипотенуз Дизайн ХХК Барилгын зураг төслийн "ГИПОТЕНУЗ ДИЗАЙН" ХХК	Гүйцэтгэгч: "Гипотенуз Дизайн" ХХК-н захирал	М.Энхтөр		М1:200
УТАС : 88014798	Гүйцэтгэгч: Архитектор	Б.Ариунзаяа		Хуудас-17
	Захиалагч: Боловсролын яамны Санхүү, хөрөнгө оруулалтын хэлтсийн дарга	Х.Тамираа		2025 он

3-р ДАВХРЫН БАЙГУУЛАЛТ М1:200

ӨРӨӨНИЙ ТОДОРХОЙЛОЛТ		
	Өрөө, тасалгааны нэр	Талбай ($м^2$)
1	Шатны хонгил	23.75
2	Зорчих хэсэг /коридор/	417.19
3	Эрхлэгчийн өрөө	21.84
4	Захиргаа аж ахуйн, нягтлан бодогчийн асуудал хариуцсан ажилтнуудын өрөө	17.68
5	Захирлын өрөө	20.28
6	Бичиг хэрэг хяналтын ажилтан	21.55
7	Зохион байгуулагч, Техникийн ажилтаны өрөө	38.12
8	Хувцасны өлгүүр	18.93
9	6-12-р анги хичээлийн танхим	75.66
10	6-12-р анги хичээлийн танхим	78.32
11	АЦӨ Я.Х.Х	5.26
12	Дунд ахлах булгийн АЦӨ эр	12.87
13	Дунд ахлах булгийн АЦӨ эр	9.31
14	Спорт заал 2	233.94
15	Хувцас солих өрөө	11.43
16	Хувцас солих өрөө	10.31
17	Шатны хонгил	28.92
18	Мэдээлэлзүйн хичээлийн Лаборатори	29.95
19	6-12-р анги хичээлийн танхим /мэдээлэлзүй/	103.78
20	6-12-р анги хичээлийн танхим	75.72
21	Физик хичээлийн Лаборатори	18.49
22	6-12-р анги хичээлийн танхим /физик/	96.82

Түлхүүр байгууламт

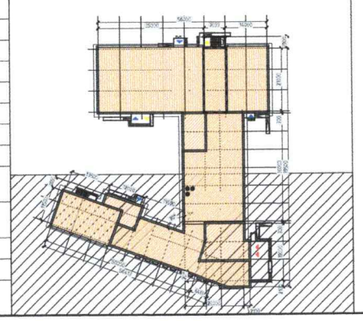

Hypotenuse Design LLC Барилгын зураг төслийн "ГИПОТЕНУЗ ДИЗАЙН" ХХК	640 ХҮҮХДИЙН СУРГУУЛИЙН БАРИЛГЫН НЭГ МАЯГИЙН ЗУРАГ ТӨСӨЛ	НЭР	ГАРЫН ҮСЭГ	ЗАГВАР ЗУРАГ
УТАС : 88014798	Гүйцэтгэгч: "Гипотенуз Дизайн" ХХК-н захирал	М.Энхтөр		М1:200
	Гүйцэтгэгч: Архитектор	Б.Ариунзаяа		Хуудас-18
	Захиалагч: Боловсролын яамны Санхүү, хөрөнгө оруулалтын хэлтсийн дарга	Х.Тамираа		2025 он

З-р ДАВХРЫН БАЙГУУЛАЛТ М1:200

ӨРӨӨНИЙ ТОДОРХОЙЛОЛТ		
	Өрөө, тасалгааны нэр	Талбай ($м^2$)
23	6-12-р анги хичээлийн танхим /лингафон/	75.05
24	6-12-р анги хичээлийн танхим	75.12
25	Дунд ахлах булгийн АЦӨ эр	13.80
26	АЦӨ эм	8.38
27	Дунд ахлах булгийн АЦӨ эм	13.46
28	АЦӨ Я.Х.Х	5.25
29	Шатны хонгил	24.54
30	Зорчих хэсэг /коридор/	61.38
31	Цэвэрлэгээний тоног төхөөрөмж хадгалах өрөө	7.05
32	Багш нарийн өрөө	14.61
33	Спорт заалны агуулах	20.43
34	Урлаг заалны агуулах	23.74
35	Спорт заалны суудал	38.76
36	Зугтах гарцын гонх	7.25
	Нийт талбай	1758.94
	Тэнхлэгийн талбай	1900.65

Түлхүүр байгууламт

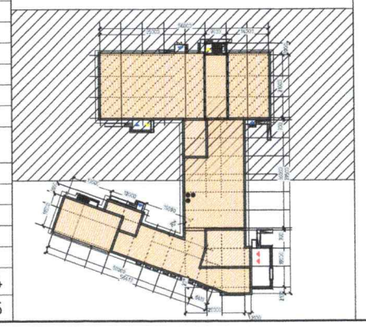

ГАЛ ТҮЙМРИЙН УХТ БАЙЦААЛАЛ ОБЪ

Барилгын зураг төслийн "ГИПОТЕНУЗ ДИЗАЙН" ХХК УТАС : 88014798	640 ХҮҮХДИЙН СУРГУУЛИЙН БАРИЛГЫН НЭГ МАЯГИЙН ЗУРАГ ТӨСӨЛ	НЭР	ГАРЫН ҮСЭГ	ЗАГВАР ЗУРАГ
	Гүйцэтгэгч: "Гипотенуз Дизайн" ХХК-н захирал	М.Энхтөр		М1:200
	Гүйцэтгэгч: Архитектор	Б.Ариунзаяа		Хуудас-19
	Захиалагч: Боловсролын яамны Санхүү, хөрөнгө оруулалтын хэлтсийн дарга	Х.Тамираа		2025 он

ТЕХНИКИЙН ДАВХРЫН БАЙГУУЛАЛТ М1:200

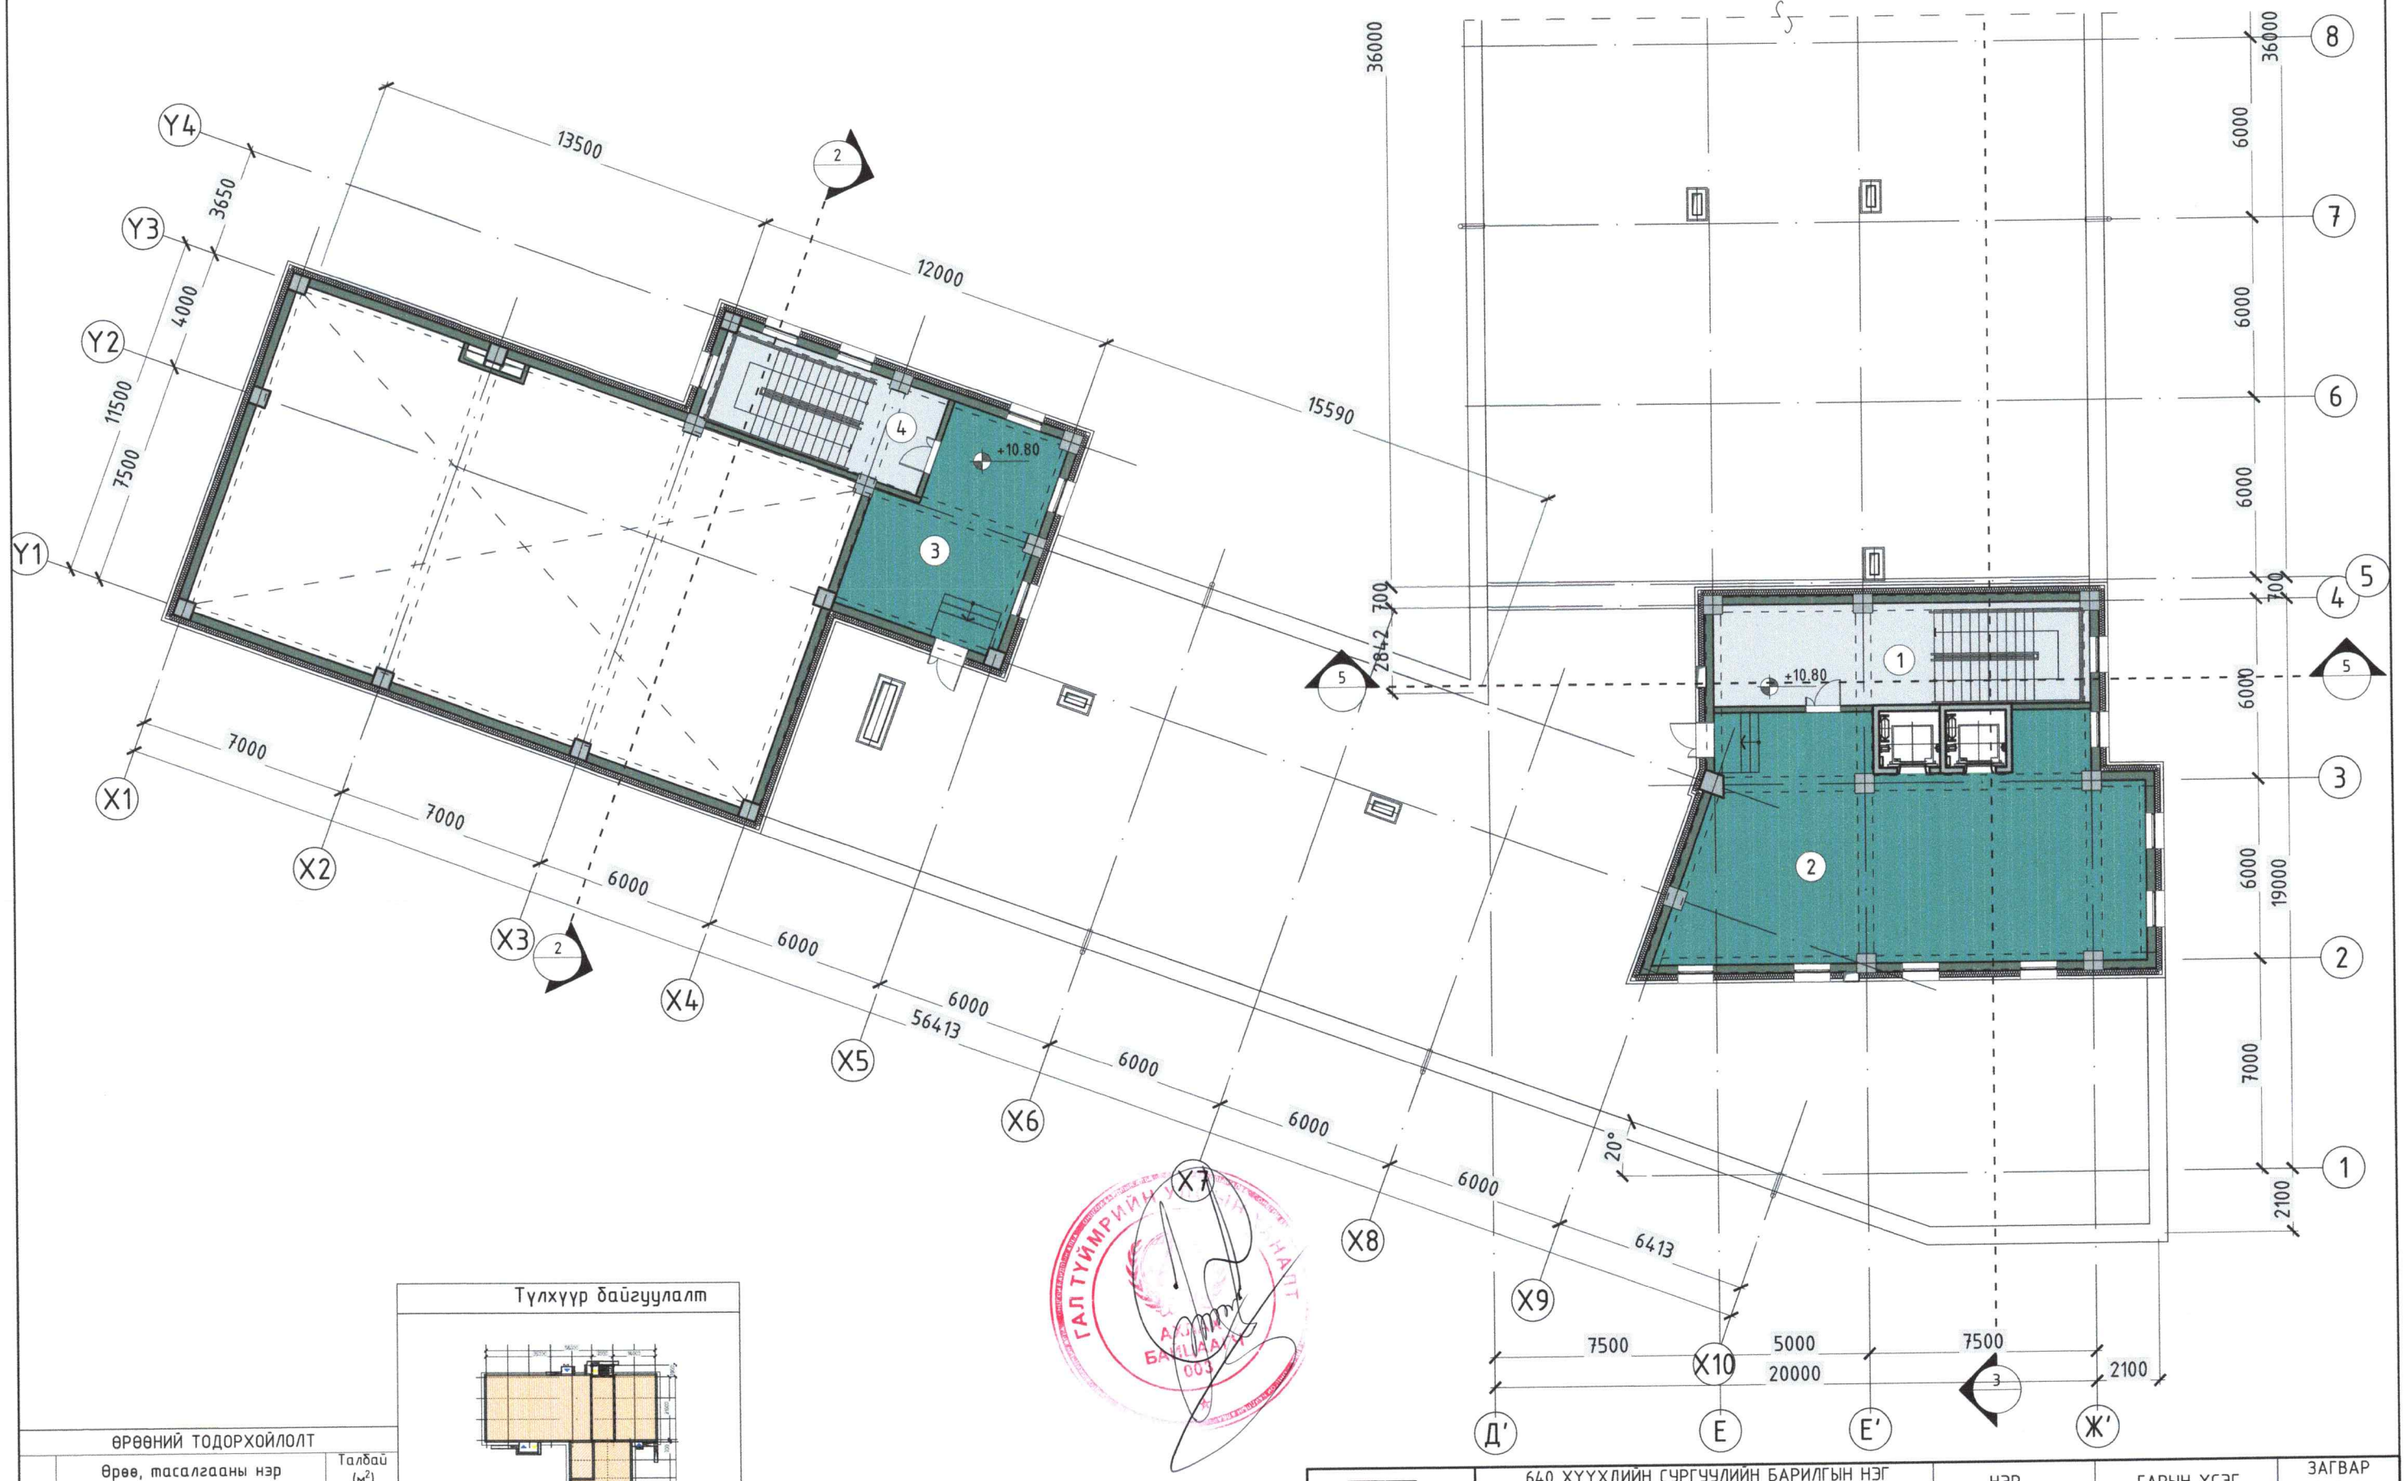

Түлхүүр байгууламт

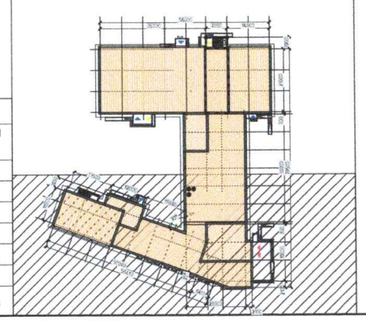

ӨРӨӨНИЙ ТОДОРХОЙЛОЛТ		
	Өрөө, тасалгааны нэр	Талбай ($м^2$)
1	Шатны хонгил	42.14
2	Техникийн өрөө	111.29
3	Техникийн өрөө	37.48
4	Шатны хонгил	25.86
5	Техникийн өрөө	62.46
6	Шатны хонгил	25.32
	Нийт талбай	279.24

ГАЛ ТҮЙМРИЙН АЛБАН БАЙГАА ГАЗАР

Hypotenuse Design LLC Барилгын зураг төслийн "ГИПОТЕНУЗ ДИЗАЙН" ХХК УТАС : 88014798	640 ХҮҮХДИЙН СУРГУУЛИЙН БАРИЛГЫН НЭГ МАЯГИЙН ЗУРАГ ТӨСӨЛ	НЭР	ГАРЫН ҮСЭГ	ЗАГВАР ЗУРАГ
	Гүйцэтгэгч: "Гипотенуз Дизайн" ХХК-н захирал	М.Энхтөр		М1:200
	Гүйцэтгэгч: Архитектор	Б.Арцунзаяа		Хуудас-20
	Захиалагч: Боловсролын яамны Санхүү, хөрөнгө оруулалтын хэлтсийн дарга	Х.Тамираа		2025 он

ТЕХНИКИЙН ДАВХРЫН БАЙГУУЛАЛТ М1:200

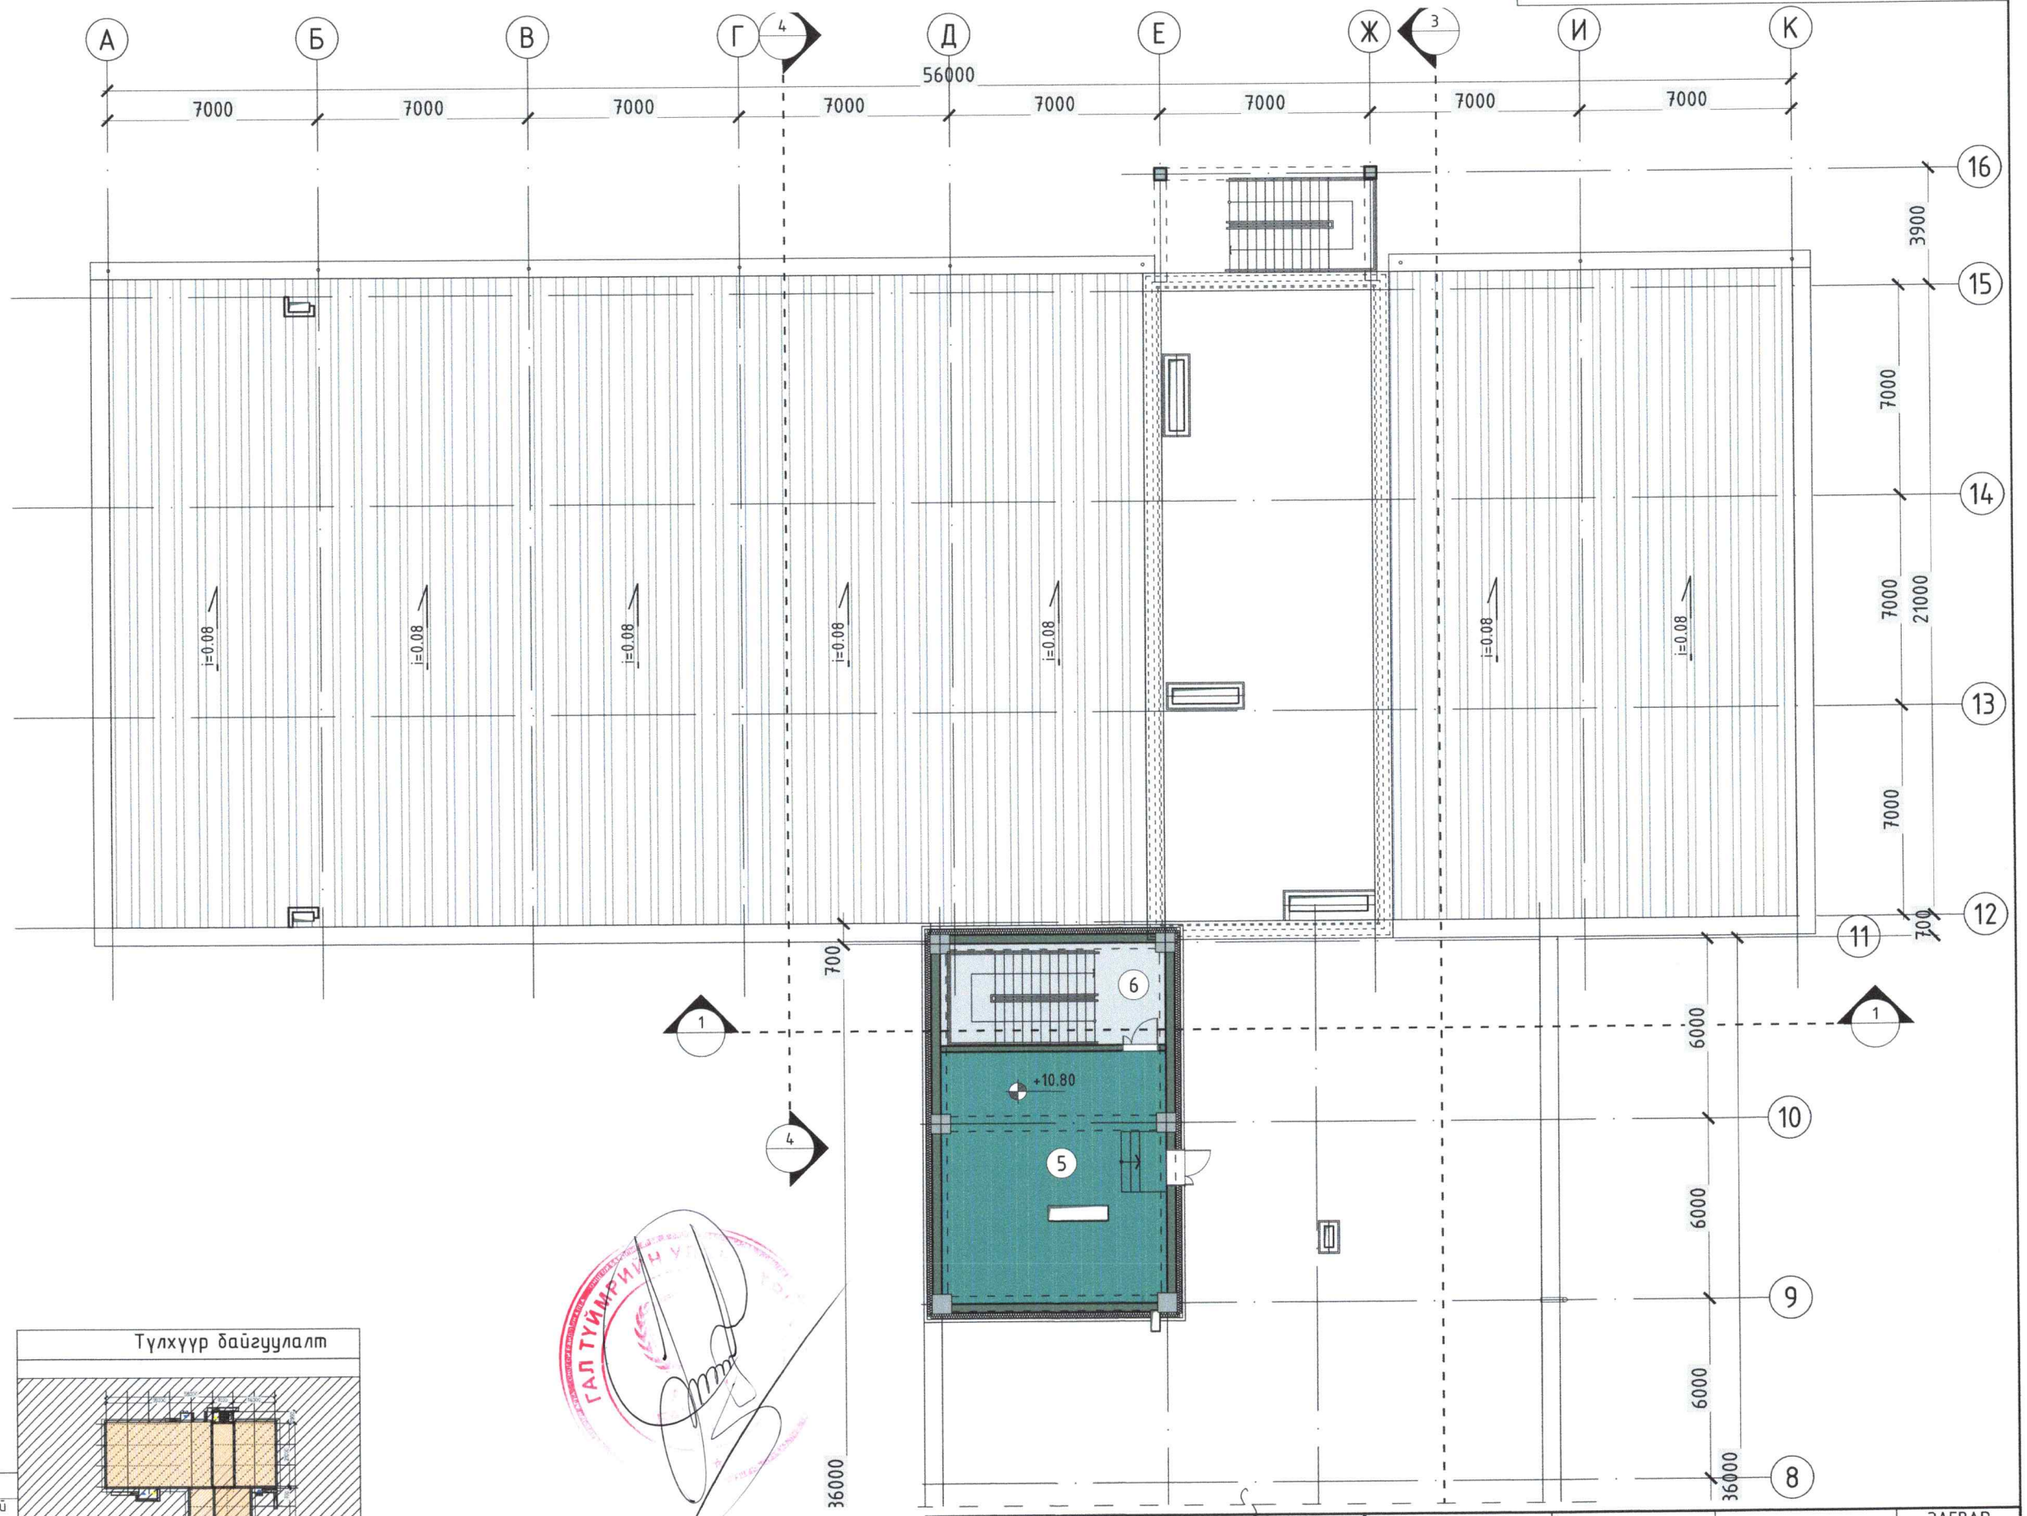

ГАЛ ТҮЙМРИЙН УУЛ

Түлхүүр байгууламт

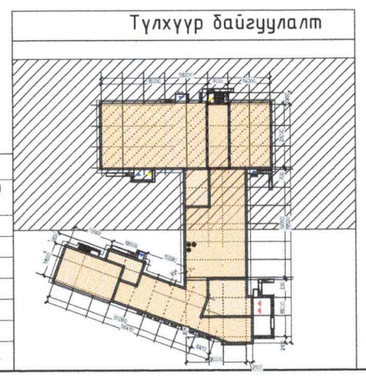

ӨРӨӨНИЙ ТОДОРХОЙЛОЛТ		
	Өрөө, тасалгааны нэр	Талбай (м²)
1	Шатны хонгил	42.14
2	Техникийн өрөө	111.29
3	Техникийн өрөө	37.48
4	Шатны хонгил	25.86
5	Техникийн өрөө	62.46
6	Шатны хонгил	25.32
	Нийт талбай	279.24

HYPOTENUSE DESIGN LLC
Барилгын зураг төслийн "ГИПОТЕНУЗ ДИЗАЙН" ХХК

УТАС : 88014798

640 ХҮҮХДИЙН СУРГУУЛИЙН БАРИЛГЫН НЭГ МАЯГИЙН ЗУРАГ ТӨСӨЛ	НЭР	ГАРЫН ҮСЭГ	ЗАГВАР ЗУРАГ
Гүйцэтгэгч: "Гипотенуз Дизайн" ХХК-н захирал	М.Энхтөр		М1:200
Гүйцэтгэгч: Архитектор	Б.Ариунзаяа		Хуудас-21
Захиалагч: Боловсролын яамны Санхүү, хөрөнгө оруулалтын хэлтсийн дарга	Х.Тамираа		2025 он

ОГТЛОЛ 1-1 М1:200

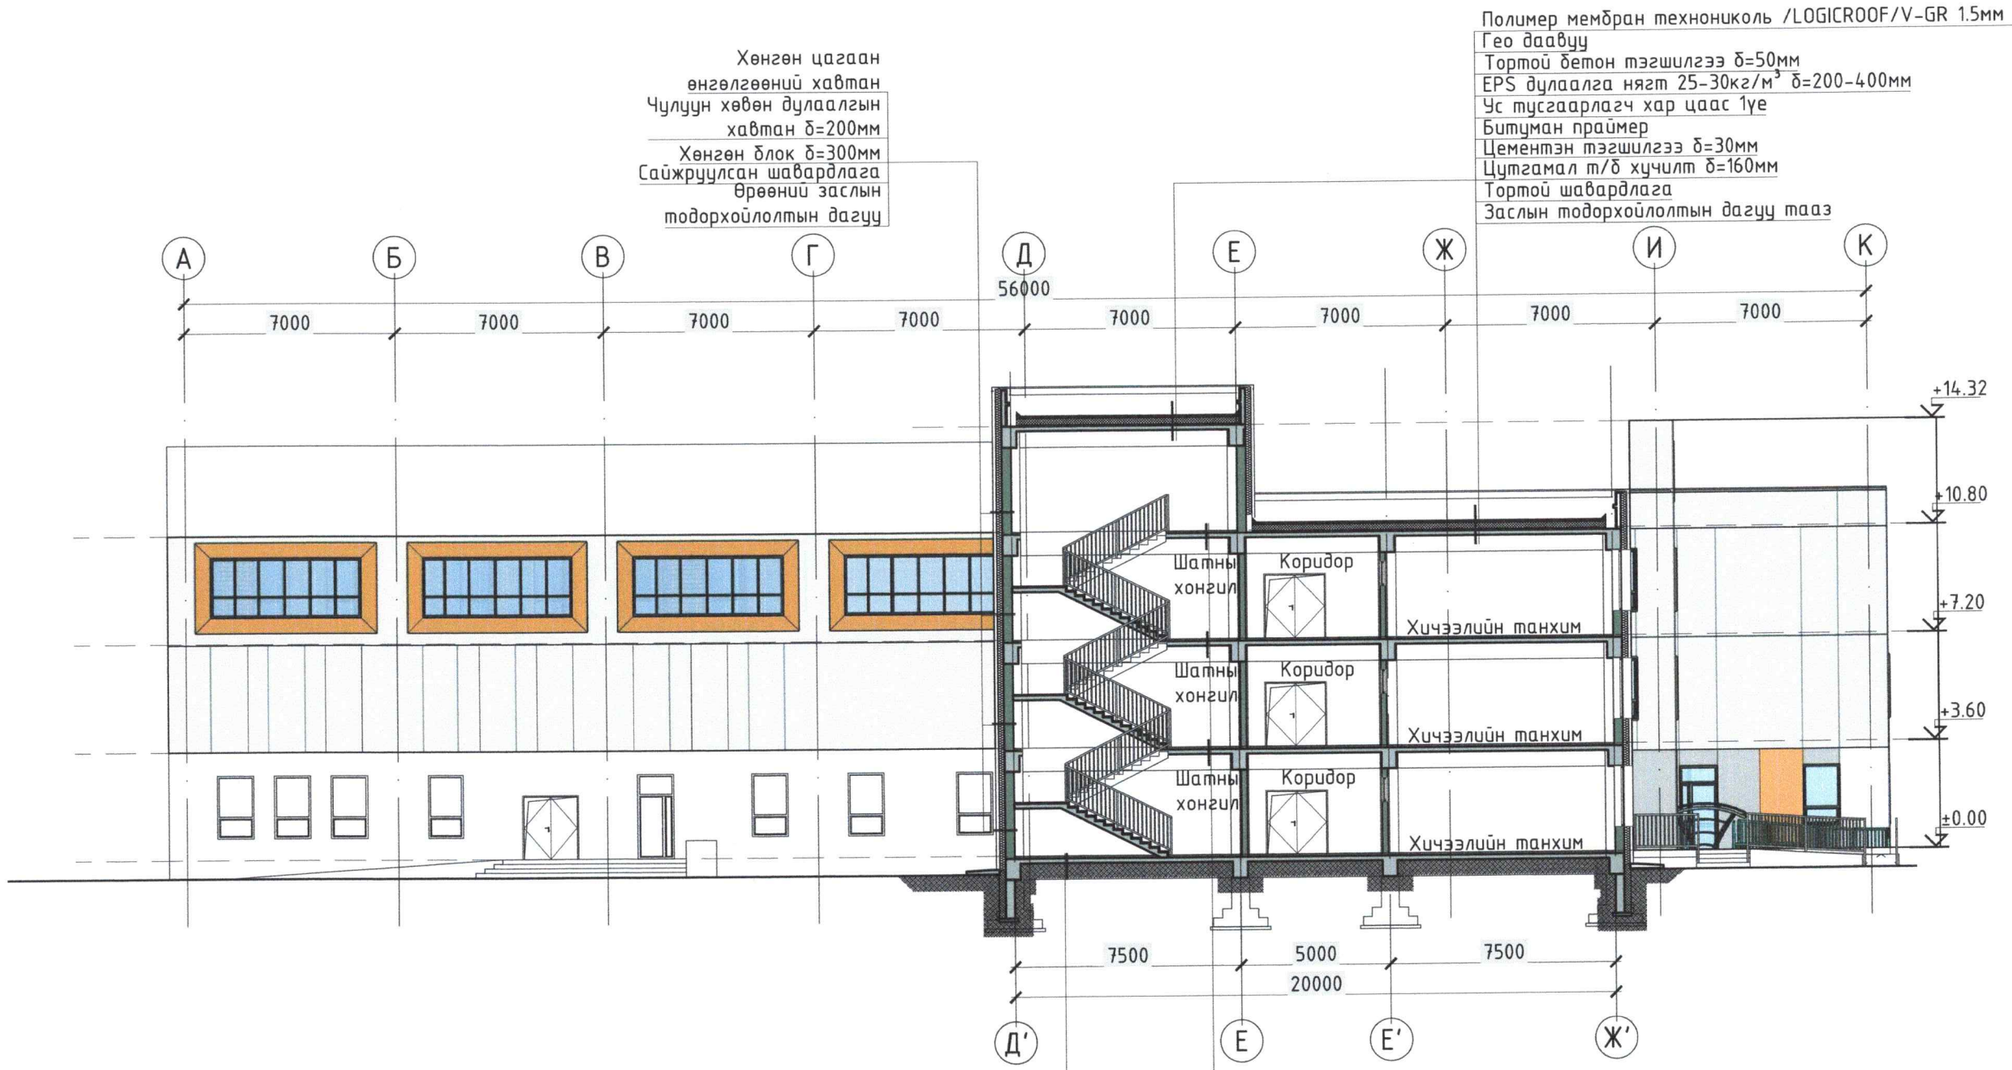

Өрөөний заслын тодорхойлолтын дагуу
Бетон тэгшилгээ δ=80мм
Цутгамал хучилт δ=160мм
XPS дулаалга δ=100мм
Ус тусгаарлагч
Нягтаршуулсан хөрс

Өрөөний заслын тодорхойлолтын дагуу
Бетон тэгшилгээ δ=60-70мм
Төмөр бетон цутгамал хучилт δ=160мм
Ус тусгаарлагч
Нягтаршуулсан хөрс

Түлхүүр байгууламт

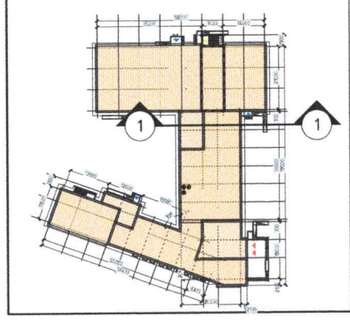

Hypotenuse Design LLC Барилгын зураг төслийн "ГИПОТЕНУЗ ДИЗАЙН" ХХК	640 ХҮҮХДИЙН СУРГУУЛИЙН БАРИЛГЫН НЭГ МАЯГИЙН ЗУРАГ ТӨСӨЛ	НЭР	ГАРЫН ҮСЭГ	ЗАГВАР ЗУРАГ
	Гүйцэтгэгч: "Гипотенуз Дизайн" ХХК-н захирал	М.Энхтөр		М1:200
	Гүйцэтгэгч: Архитектор	Б.Ариунзаяа		Хуудас-22
УТАС : 88014798	Захиалагч: Боловсролын яамны Санхүү, хөрөнгө оруулалтын хэлтсийн дарга	Х.Тамираа		2025 он

ОГТЛОЛ 4-4 М1:200

Түлхүүр байгууламт

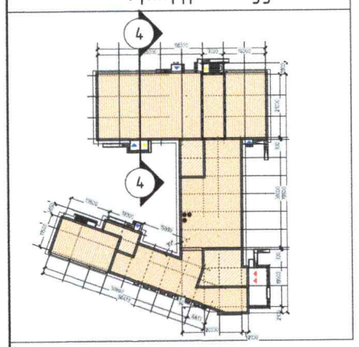

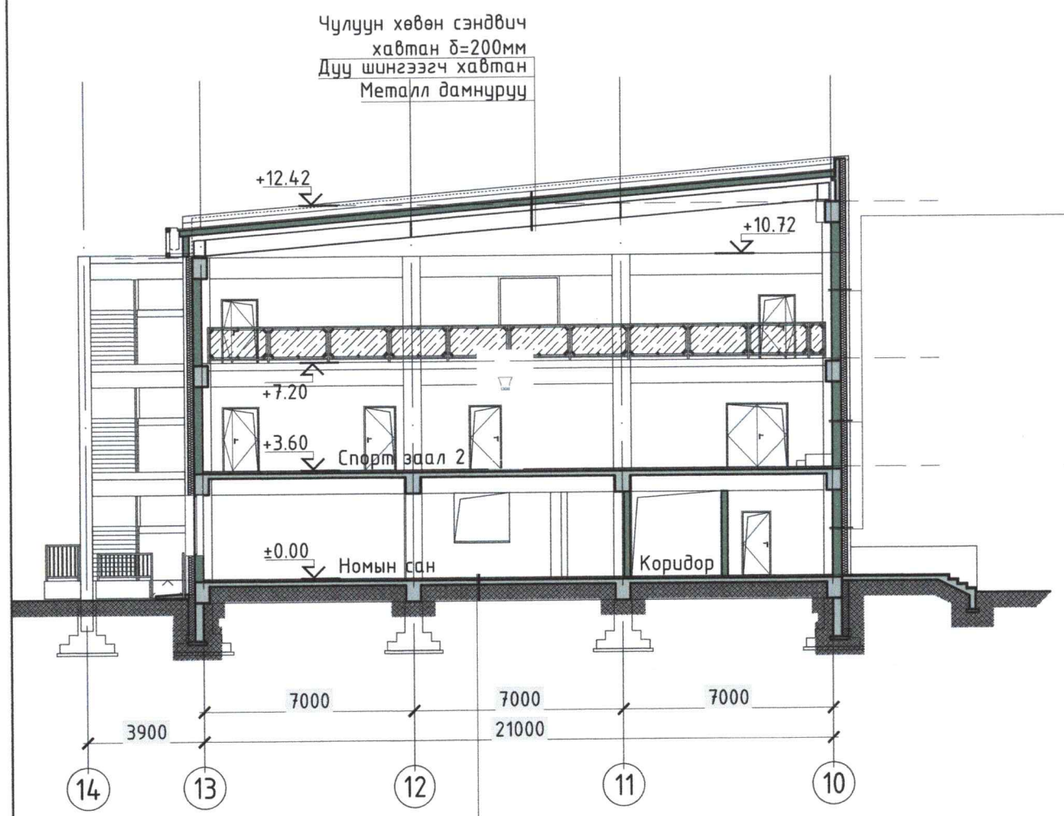

ОГТЛОЛ 2-2 М1:200

Түлхүүр байгууламт

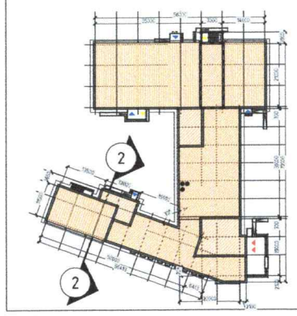

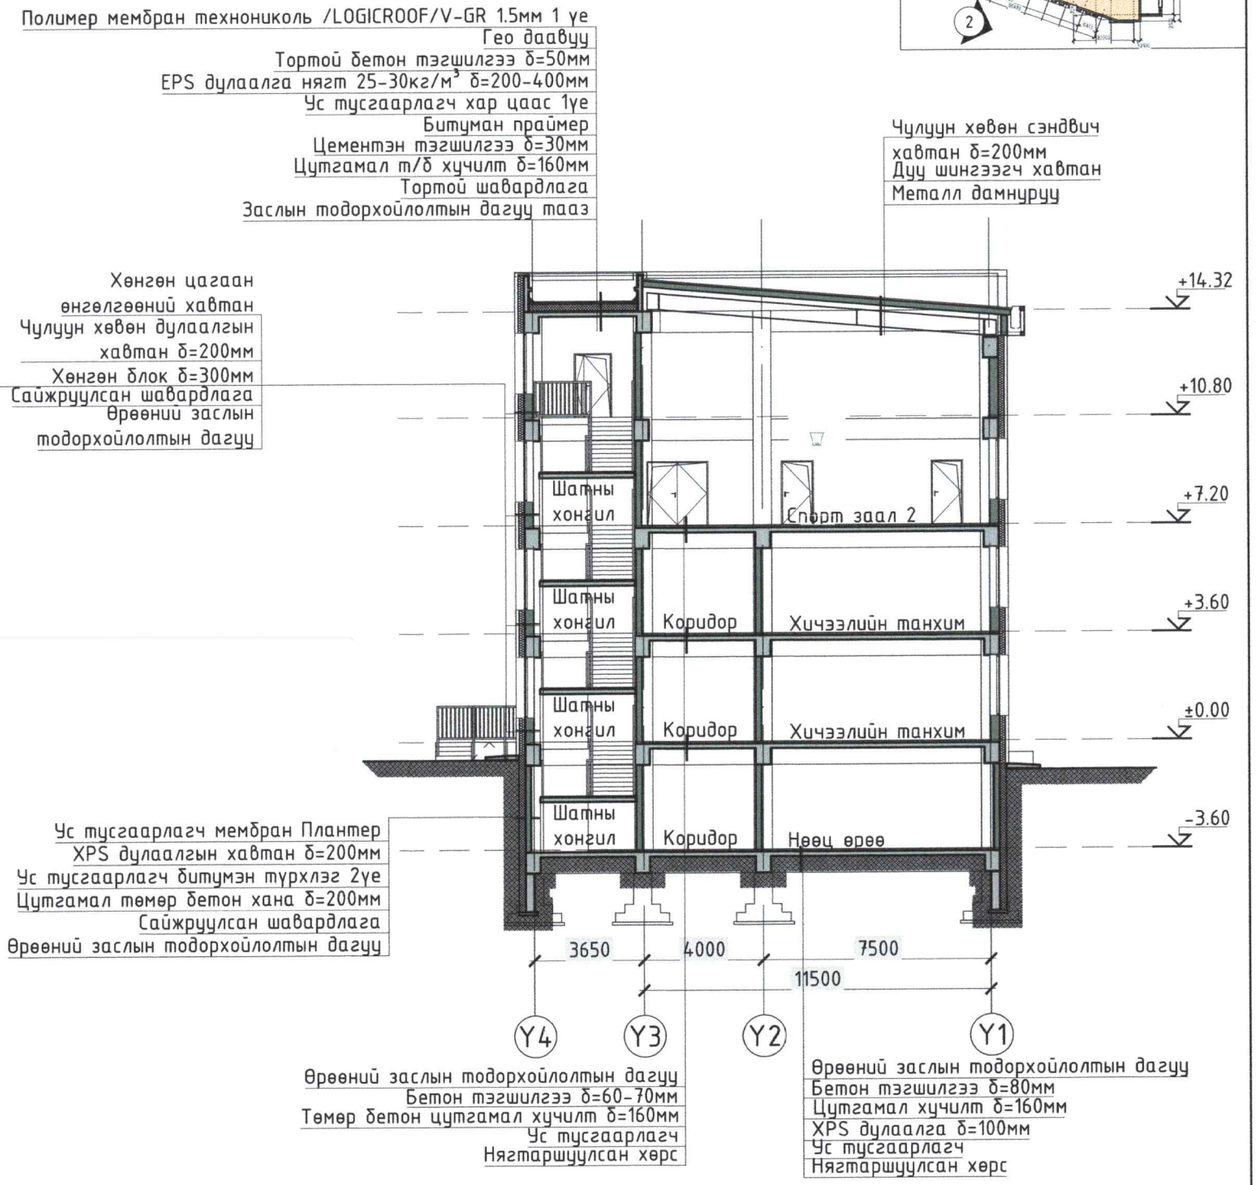

Барилгын зураг төслийн "ГИПОТЕНУЗ ДИЗАЙН" ХХК	640 ХҮҮХДИЙН СУРГУУЛИЙН БАРИЛГЫН НЭГ МАЯГИЙН ЗУРАГ ТӨСӨЛ	НЭР	ГАРЫН ҮСЭГ	ЗАГВАР ЗУРАГ
	Гүйцэтгэгч: "Гипотенуз Дизайн" ХХК-н захирал	М.Энхтөр		М1:200
	Гүйцэтгэгч: Архитектор	Б.Ариунзаяа		Хуудас-23
УТАС : 88014798	Захиалагч: Боловсролын яамны Санхүү, хөрөнгө оруулалтын хэлтсийн дарга	Х.Тамираа		2025 он

ОГТЛОЛ 3-3 М1:200

Полимер мембран технониколь /LOGICROOF/V-GR 1.5мм 1 уе
Гео даавуу
Тортой бетон тэгшилгээ δ=50мм
EPS дулаалга нягт 25-30кг/м³ δ=200-400мм
Ус тусгаарлагч хар цаас 1уе
Битуман праймер
Цементэн тэгшилгээ δ=30мм
Цутгамал т/б хучилт δ=160мм
Тортой шавардлага
Заслын тодорхойлолтын дагуу таяз

+14.32
+10.80
Техникийн давхар
+7.20
+3.60
±0.00
-3.60

Өрөөний заслын тодорхойлолтын дагуу
Бетон тэгшилгээ δ=60-70мм
Цутгамал хучилт δ=160мм
Ус тусгаарлагч
Нягтаршуулсан хөрс

Өрөөний заслын тодорхойлолтын дагуу
Бетон тэгшилгээ δ=80мм
Цутгамал хучилт δ=160мм
XPS дулаалга δ=100мм
Ус тусгаарлагч
Нягтаршуулсан хөрс

6000 6000 6000 6000 6000 6000 6000
36000
700
7000 6000 6000
2100 19000 700
1 2 3 4 5 5 6 7 8 9 10

Чулуун хөвөн сэндвич хавтан δ=200мм
Дуу шингээгч хавтан
Металл дамнуруу

+10.72
+9.02
+3.60
Урлаг заал
±0.00
Коридор
Хооллох заал

7000 7000 7000
700 21000 3900
10 11 12 13 14

Түлхүүр байгууламт

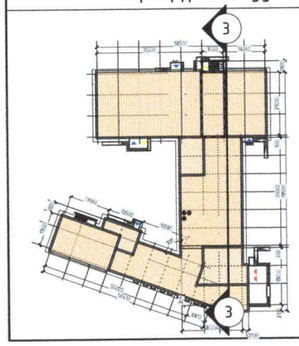

Барилгын зураг төслийн "ГИПОТЕНУЗ ДИЗАЙН" ХХК	640 ХҮҮХДИЙН СУРГУУЛИЙН БАРИЛГЫН НЭГ МАЯГИЙН ЗУРАГ ТӨСӨЛ	НЭР	ГАРЫН ҮСЭГ	ЗАГВАР ЗУРАГ
УТАС : 88014798	Гүйцэтгэгч: "Гипотенуз Дизайн" ХХК-н захирал	М.Энхтөр		М1:200
	Гүйцэтгэгч: Архитектор	Б.Ариунзаяа		Хуудас-24
	Захиалагч: Боловсролын яамны Санхүү, хөрөнгө оруулалтын хэлтсийн дарга	Х.Тамираа		2025 он

ОГТЛОЛ 5-5 М1:200

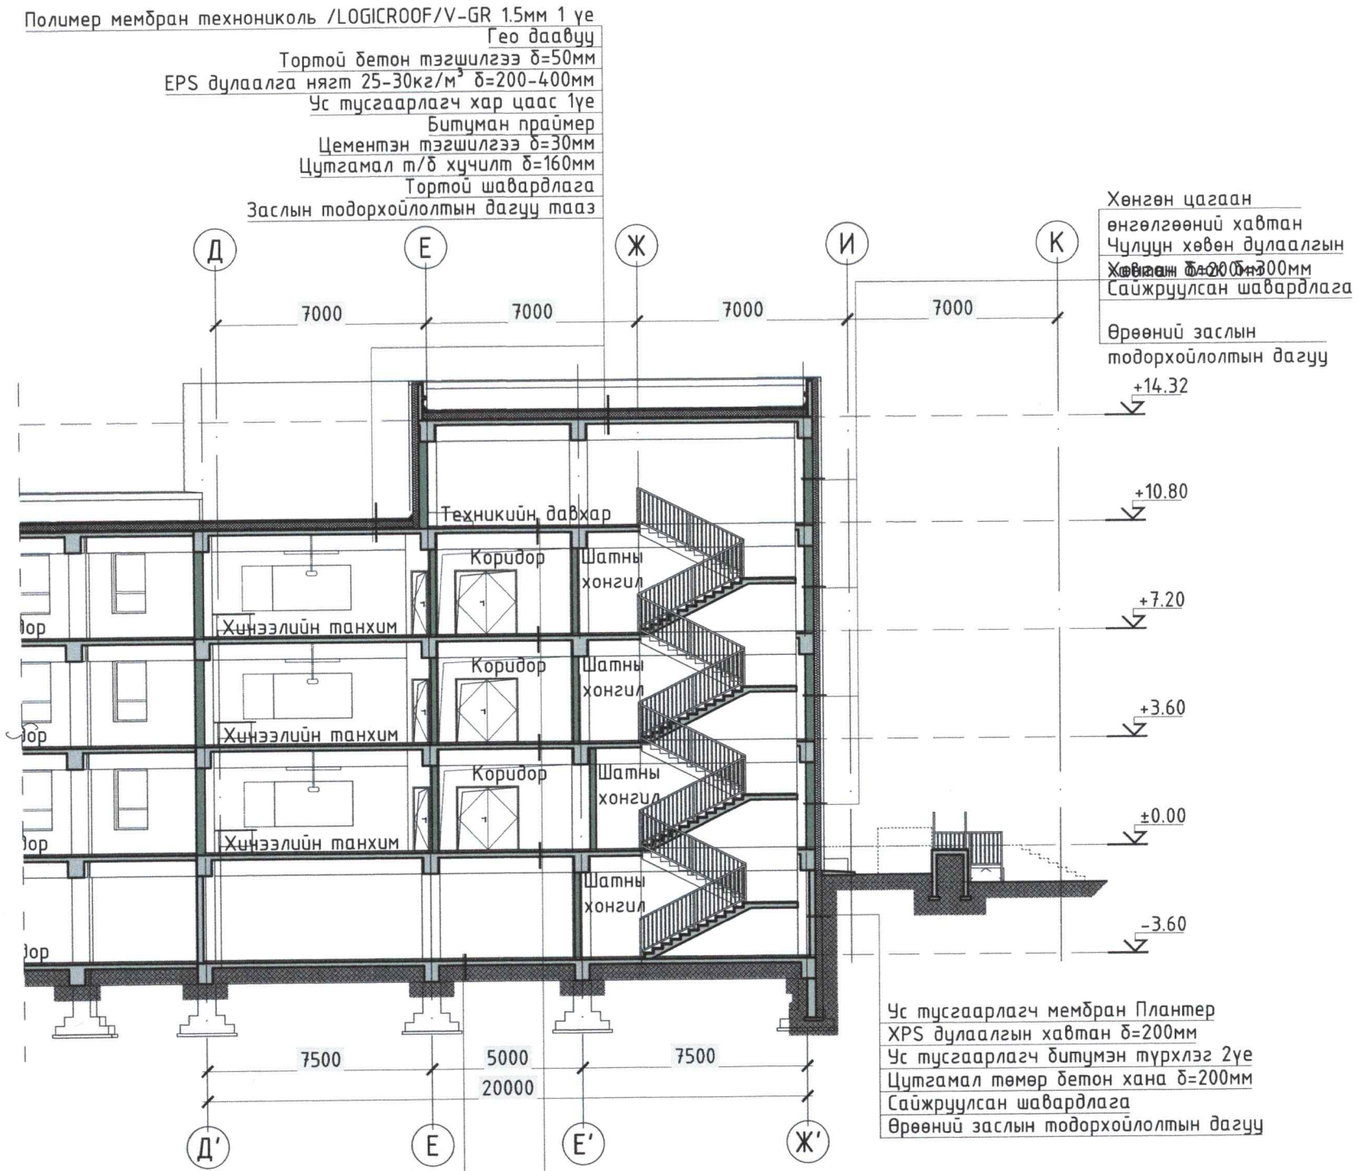

Түлхүүр байгууламт

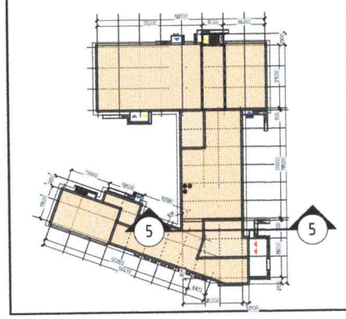

Барилгын зураг төслийн "ГИПОТЕНУЗ ДИЗАЙН" ХХК УТАС : 88014798	640 ХҮҮХДИЙН СУРГУУЛИЙН БАРИЛГЫН НЭГ МАЯГИЙН ЗУРАГ ТӨСӨЛ	НЭР	ГАРЫН ҮСЭГ	ЗАГВАР ЗУРАГ
	Гүйцэтгэгч: "Гипотенуз Дизайн" ХХК-н захирал	М.Энхтөр		М1:200
	Гүйцэтгэгч: Архитектор	Б.Ариунзаяа		Хуудас-25
	Захиалагч: Боловсролын яамны Санхүү, хөрөнгө оруулалтын хэлтсийн дарга	Х.Тамираа		2025 он

НҮҮР ТАЛ 1-14 М1:200

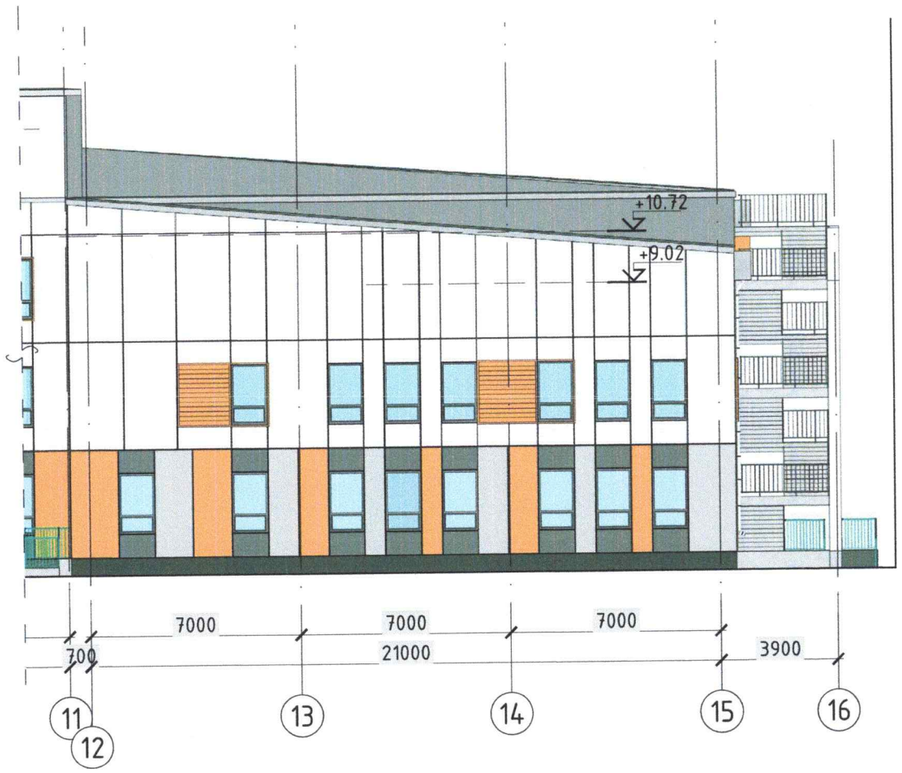

Цайвар саарал өнгийн нийлмэл хавтан / CMYK C 7 %, M 10 %, Y 29 %, K 0 %

Шар өнгийн нийлмэл хавтан / CMYK C 6 %, M 21 %, Y 48 %, K 0 %

Шар өнгийн судалтай нийлмэл хавтан / CMYK C 0 %, M 37 %, Y 69 %, K 0 %

Саарал нийлмэл хавтан / CMYK C 35 %, M 28 %, Y 28 %, K 0 %

Түлхүүр байгууламт

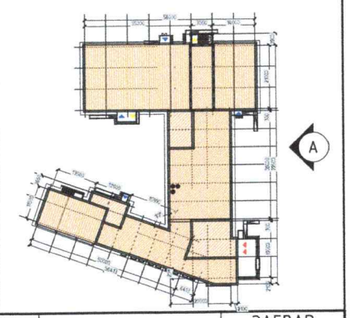

Hypotenuse Design LLC Барилгын зураг төслийн "ГИПОТЕНУЗ ДИЗАЙН" ХХК	640 ХҮҮХДИЙН СУРГУУЛИЙН БАРИЛГЫН НЭГ МАЯГИЙН ЗУРАГ ТӨСӨЛ	НЭР	ГАРЫН ҮСЭГ	ЗАГВАР ЗУРАГ
	Гүйцэтгэгч: "Гипотенуз Дизайн" ХХК-н захирал	М.Энхтөр		М1:200
	Гүйцэтгэгч: Архитектор	Б.Ариунзаяа		Хуудас-26
УТАС : 88014798	Захиалагч: Боловсролын яамны Санхүү, хөрөнгө оруулалтын хэлтсийн дарга	Х.Тамираа		2025 он

НҮҮР ТАЛ 14-1,Y1 М1:200

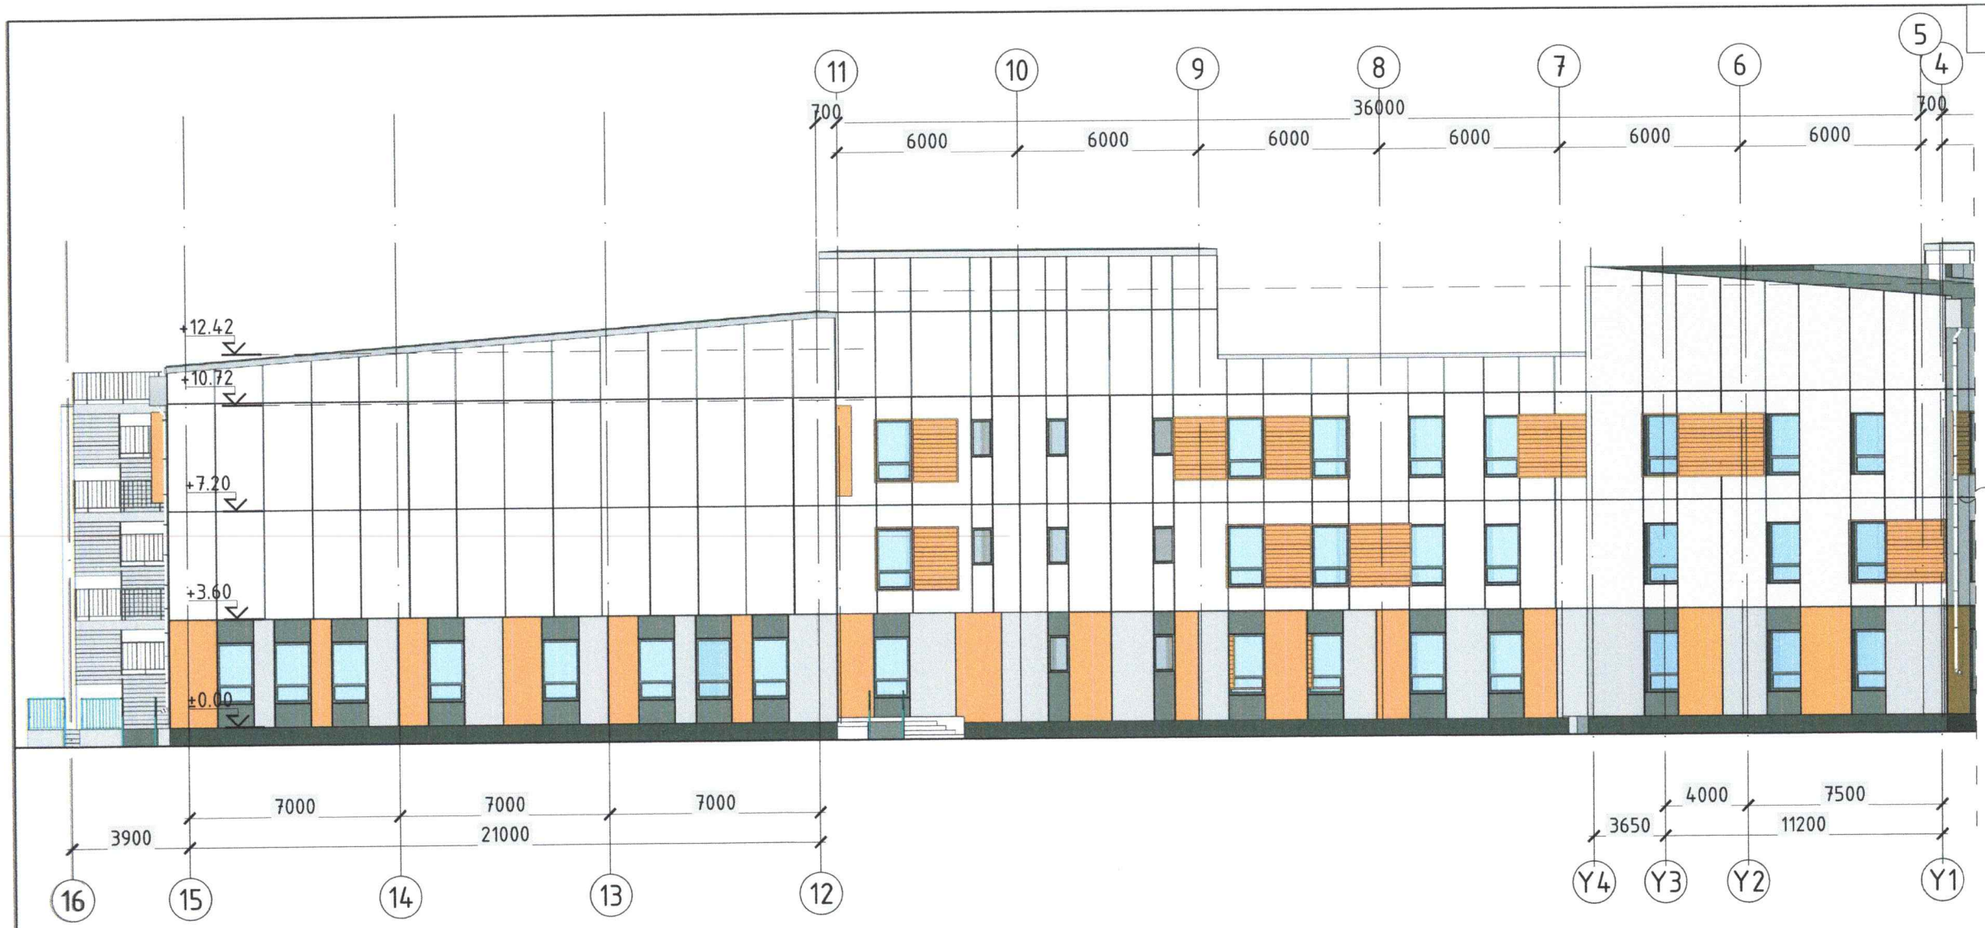

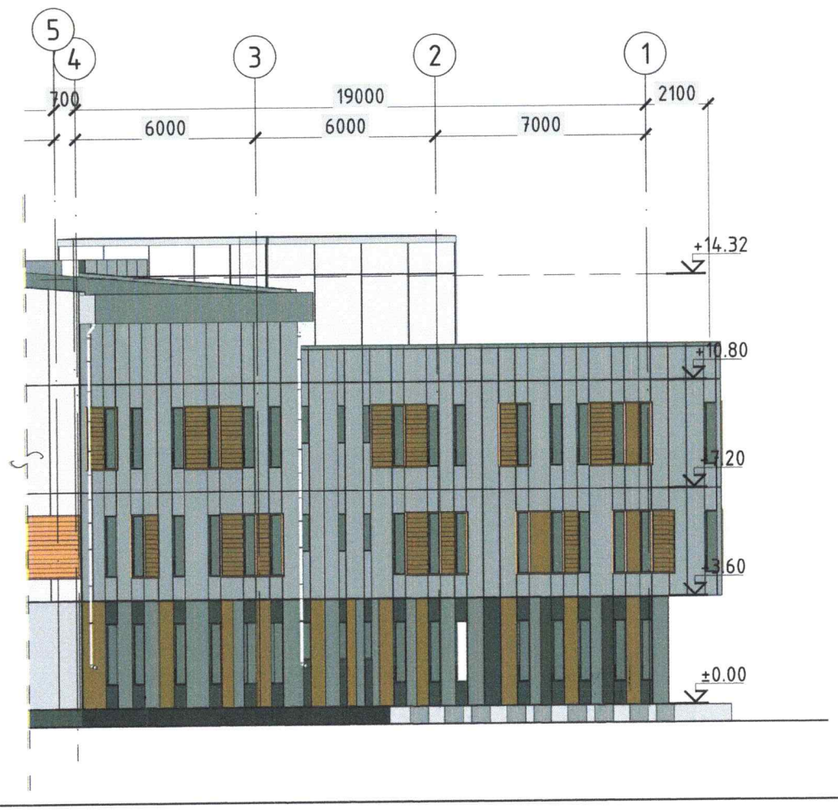

Цайвар саарал өнгийн нийлмэл хавтан / CMYK C 7 %, M 10 %, Y 29 %, K 0 %

Шар өнгийн нийлмэл хавтан / CMYK C 6 %, M 21 %, Y 48 %, K 0 %

Шар өнгийн судалтай нийлмэл хавтан / CMYK C 0 %, M 37 %, Y 69 %, K 0 %

Саарал нийлмэл хавтан / CMYK C 35 %, M 28 %, Y 28 %, K 0 %

Түлхүүр байгууламт

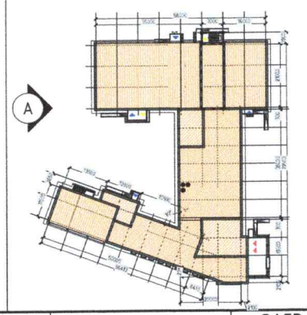

Барилгын зураг төслийн "ГИПОТЕНУЗ ДИЗАЙН" ХХК	640 ХҮҮХДИЙН СУРГУУЛИЙН БАРИЛГЫН НЭГ МАЯГИЙН ЗУРАГ ТӨСӨЛ	НЭР	ГАРЫН ҮСЭГ	ЗАГВАР ЗУРАГ
	Гүйцэтгэгч: "Гипотенуз Дизайн" ХХК-н захирал	М.Энхтөр		М1:200
	Гүйцэтгэгч: Архитектор	Б.Ариунзаяа		Хуудас-27
УТАС : 88014798	Захиалагч: Боловсролын яамны Санхүү, хөрөнгө оруулалтын хэлтсийн дарга	Х.Тамираа		2025 он

НҮҮР ТАЛ Х1-Х9,К М1:200

Түлхүүр байгууламт

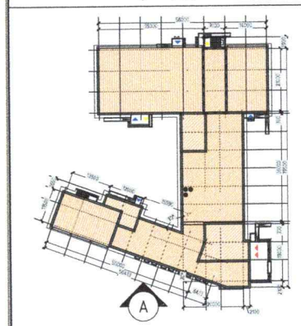

Цайвар саарал өнгийн нийлмэл хавтан / CMYK C 7 %, M 10 %, Y 29 %, K 0 %

Шар өнгийн нийлмэл хавтан / CMYK C 6 %, M 21 %, Y 48 %, K 0 %

Шар өнгийн судалтай нийлмэл хавтан / CMYK C 0 %, M 37 %, Y 69 %, K 0 %

Саарал нийлмэл хавтан / CMYK C 35 %, M 28 %, Y 28 %, K 0 %

Барилгын зураг төслийн "ГИПОТЕНУЗ ДИЗАЙН" ХХК	640 ХҮҮХДИЙН СУРГУУЛИЙН БАРИЛГЫН НЭГ МАЯГИЙН ЗУРАГ ТӨСӨЛ	НЭР	ГАРЫН ҮСЭГ	ЗАГВАР ЗУРАГ
УТАС : 88014798	Гүйцэтгэгч: "Гипотенуз Дизайн" ХХК-н захирал	М.Энхтөр		М1:200
	Гүйцэтгэгч: Архитектор	Б.Ариунзаяа		Хуудас-28
	Захиалагч: Боловсролын яамны Санхүү, хөрөнгө оруулалтын хэлтсийн дарга	Х.Тамираа		2025 он

НҮҮР ТАЛ К-А М1:200

Түлхүүр байгууламт

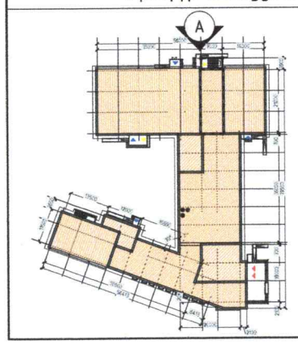

Цайвар саарал өнгийн нийлмэл хавтан / CMYK C 7 %, M 10 %, Y 29 %, K 0 %

Шар өнгийн нийлмэл хавтан / CMYK C 6 %, M 21 %, Y 48 %, K 0 %

Шар өнгийн судалтай нийлмэл хавтан / CMYK C 0 %, M 37 %, Y 69 %, K 0 %

Саарал нийлмэл хавтан / CMYK C 35 %, M 28 %, Y 28 %, K 0 %

HYPOTENUSE DESIGN LLC Барилгын зураг төслийн "ГИПОТЕНУЗ ДИЗАЙН" ХХК УТАС : 88014798	640 ХҮҮХДИЙН СУРГУУЛИЙН БАРИЛГЫН НЭГ МАЯГИЙН ЗУРАГ ТӨСӨЛ	НЭР	ГАРЫН ҮСЭГ	ЗАГВАР ЗУРАГ
	Гүйцэтгэгч: "Гипотенуз Дизайн" ХХК-н захирал	М.Энхтөр		М1:200
	Гүйцэтгэгч: Архитектор	Б.Ариунзаяа		Хуудас- 29
	Захиалагч: Боловсролын яамны Санхүү, хөрөнгө оруулалтын хэлтсийн дарга	Х.Тамираа		2025 он